



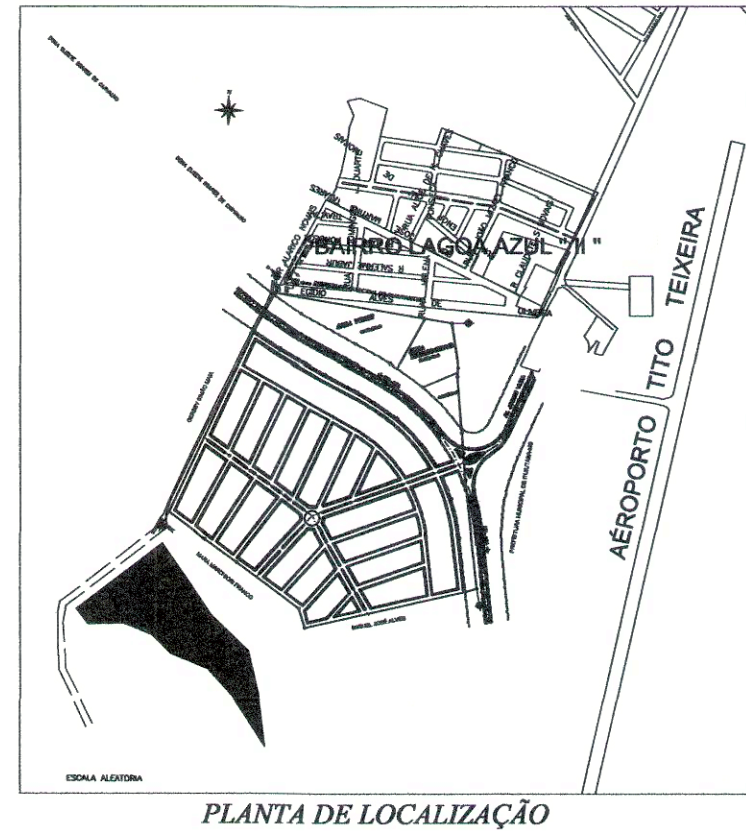


PLANTA DE LOCALIZAÇÃO

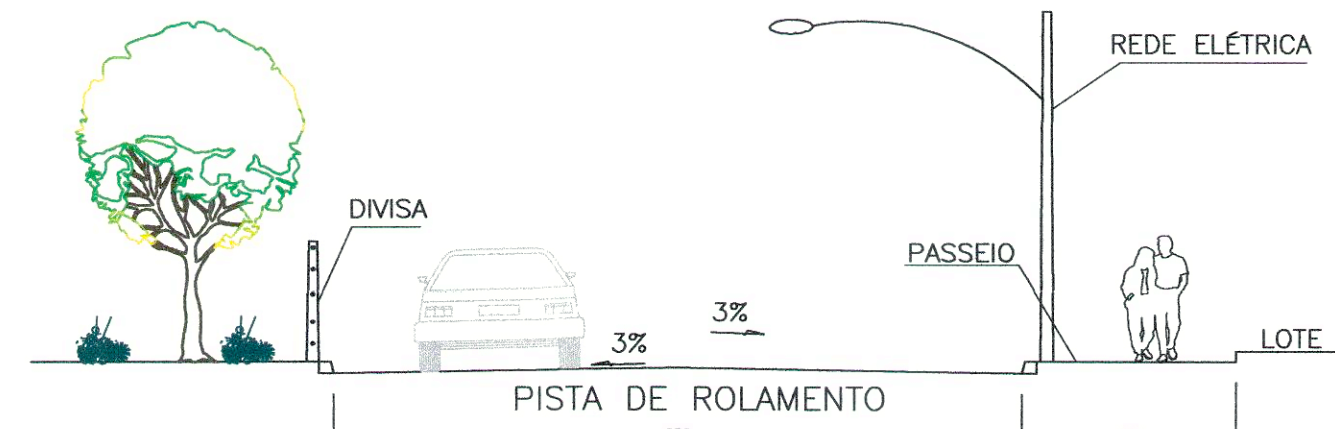


SEÇÃO TRANSVERSAL - RUAS 10.00m
RUA JL 1, JL 14, JL 15




SEÇÃO TRANSVERSAL - RUAS 25.00m
AVENIDA SANTOS DUMONT
AVENIDA TIJUCANA

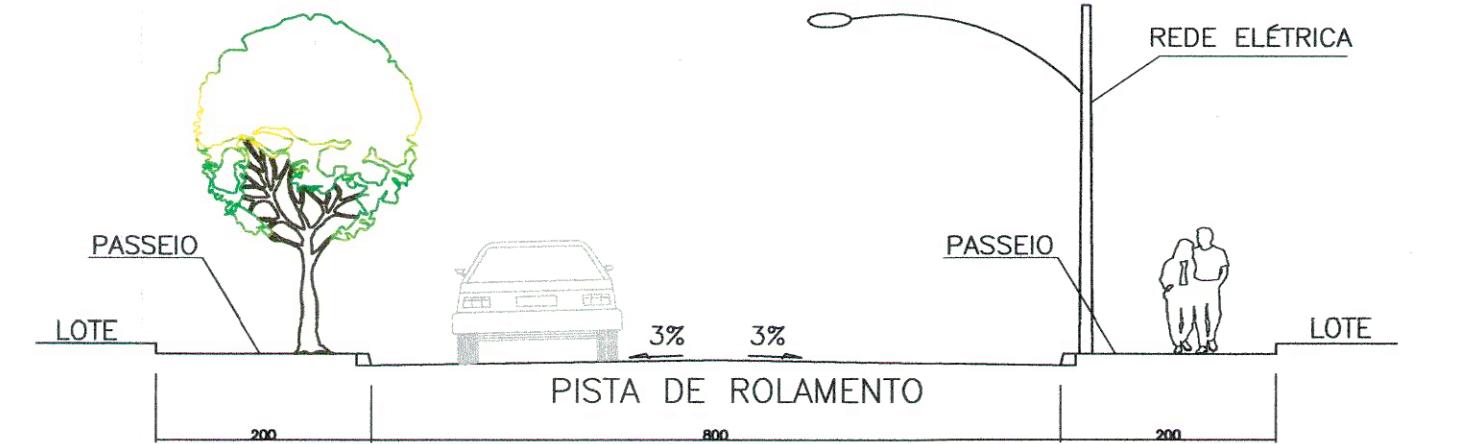

SEÇÃO TRANSVERSAL - RUAS 12.00m
RUA JL 2, JL 3, JL 4, JL 5, JL 6, JL 7
JL 8, JL 9, JL 10, JL 11, JL 12, JL 13, JL 16

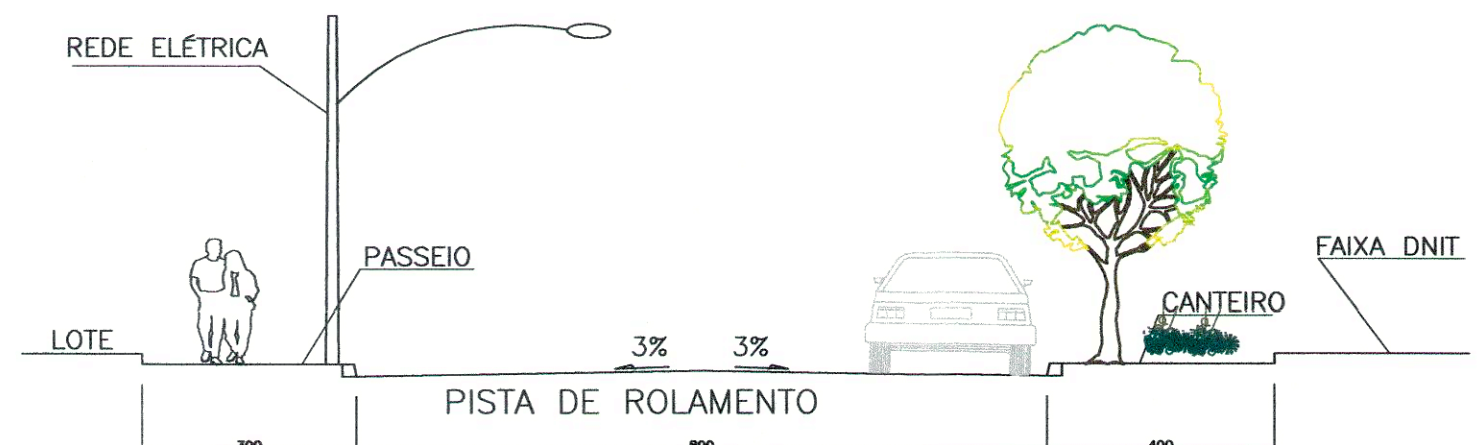

SEÇÃO TRANSVERSAL - RUAS 15.00m
RUA JL 17

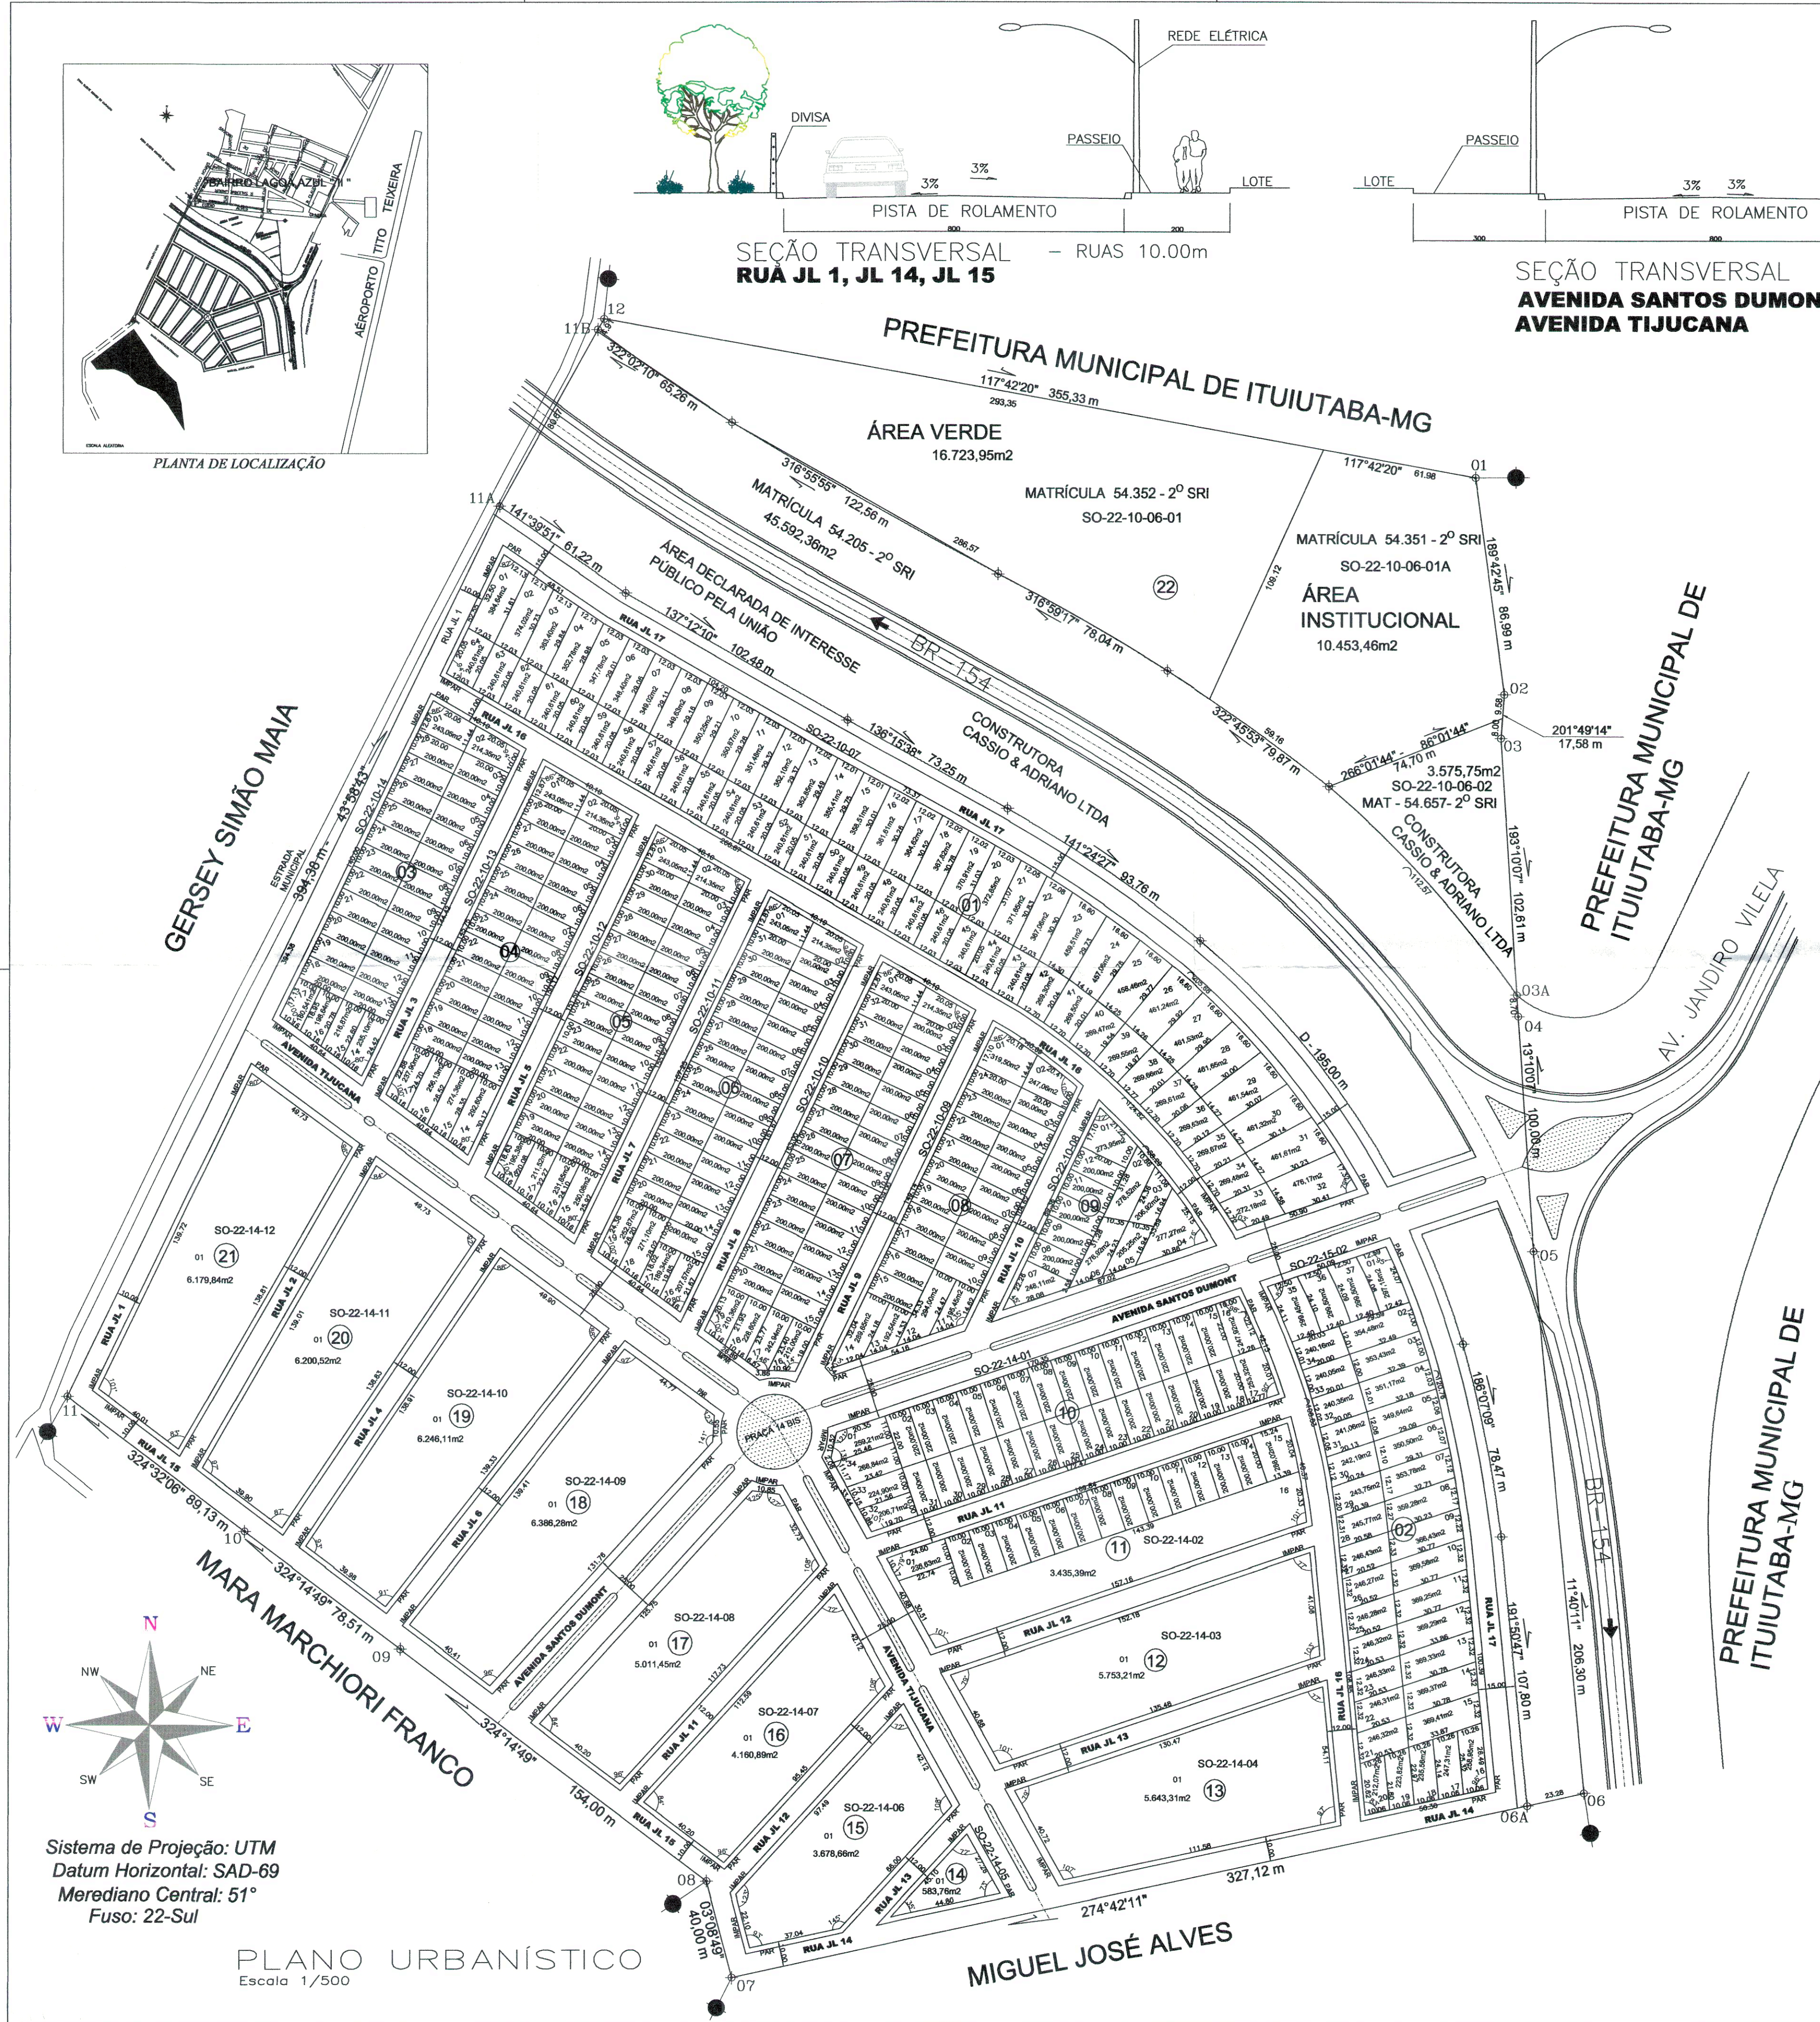

VISTOS E APROVAÇÕES

PREFEITURA MUNICIPAL DE ITUIUTABA
SECRETARIA DE PLANEJAMENTO
PLANO URBANÍSTICO APROVADO
Processo nº 13.106 / 2016
Decreto nº 8.212 / 2016 / 8.995 / 2019
Data 08/01/2019
Vicente de Paula Fontoura Filho
Secretário Municipal de Planejamento

ASSINATURAS PROJETO R.T. PROPRIETÁRIO: CONSTRUTORA CASSIO & ADRIANO LTDA
CNPJ : 03.567.677/0001-02
CARLO ALBERTO DE NOVAIS SOUZA
ARQUITETO E URBANISTA
CAU A88823-0
ADRIANO CORDEIRO
CASSIO CORDEIRO

OBSERVAÇÃO Número total de lotes - 346 REVISÃO R-01 DES. Clarivan DATA 01/04/2016

LOCALIZAÇÃO Antiga Fazenda do Carmo às margens da BR 154 Próximo ao Aeroporto Tito Teixeira Ituiutaba - MG MATRÍCULAS : 54.626-2ºSRI 55.352-2ºSRI 55.351-2ºSRI

PLANO URBANÍSTICO		
LOTEAMENTO RESIDENCIAL JOAQUIM LEME		
CONTEÚDO	FOLHA	ÚNICA
ESPECIFICAÇÃO	ÁREA (m2)	%
1 - Área total de lotes	133.707,92	63,82
2 - Sistema Viário	75.341,56	36,18
5 - Área Loteada - Matrícula 54.206 - 2º SRI	209.049,48	100,0
4 - Área Institucional - Matrícula 55.351 - 2º SRI	10.453,46	5,0
5 - Área Verde - Matrícula 55.352 - 2º SRI	16.723,95	8,0
6 - TOTAL Matrícula 54.206, 55.352 e 55.351	236.226,89	100,0

CARLO ALBERTO DE NOVAIS SOUZA
ARQUITETO E URBANISTA
CAU A88823-0