

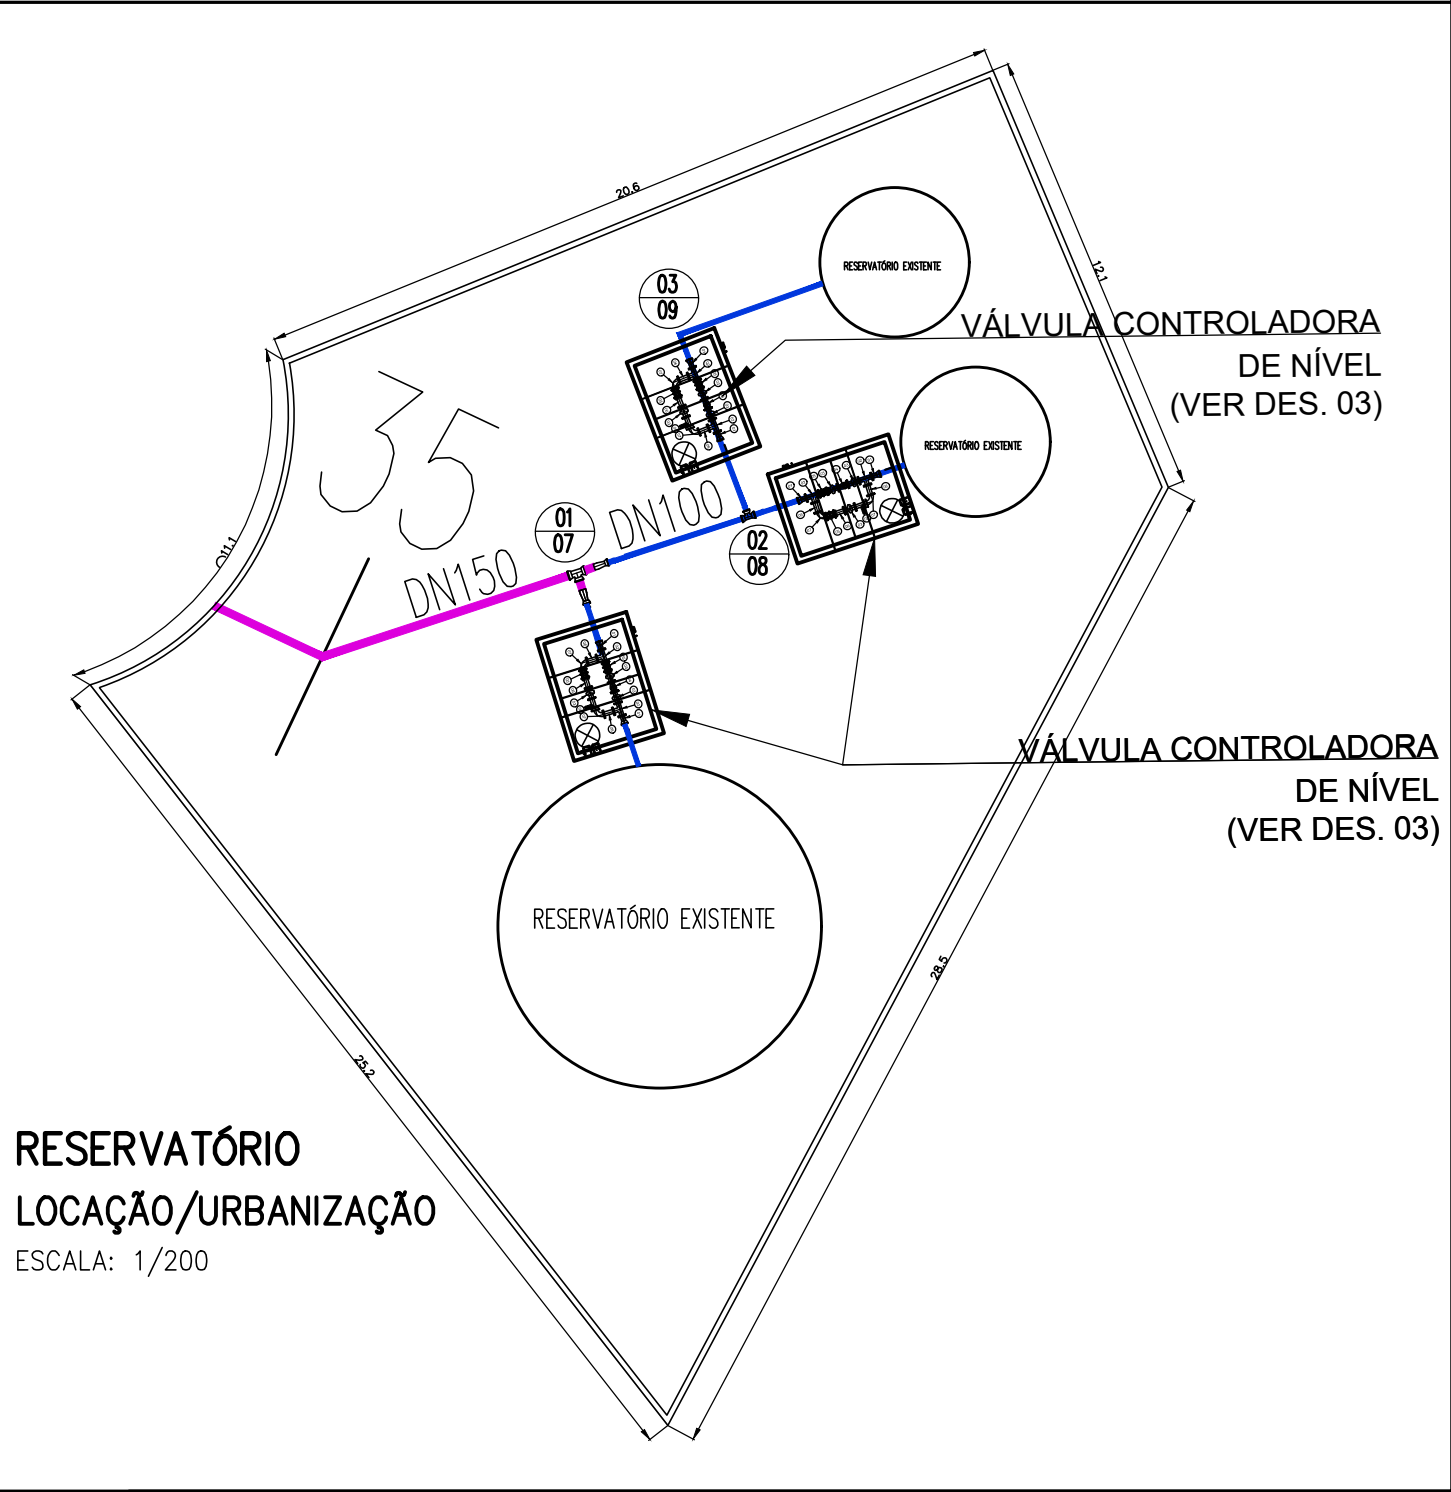


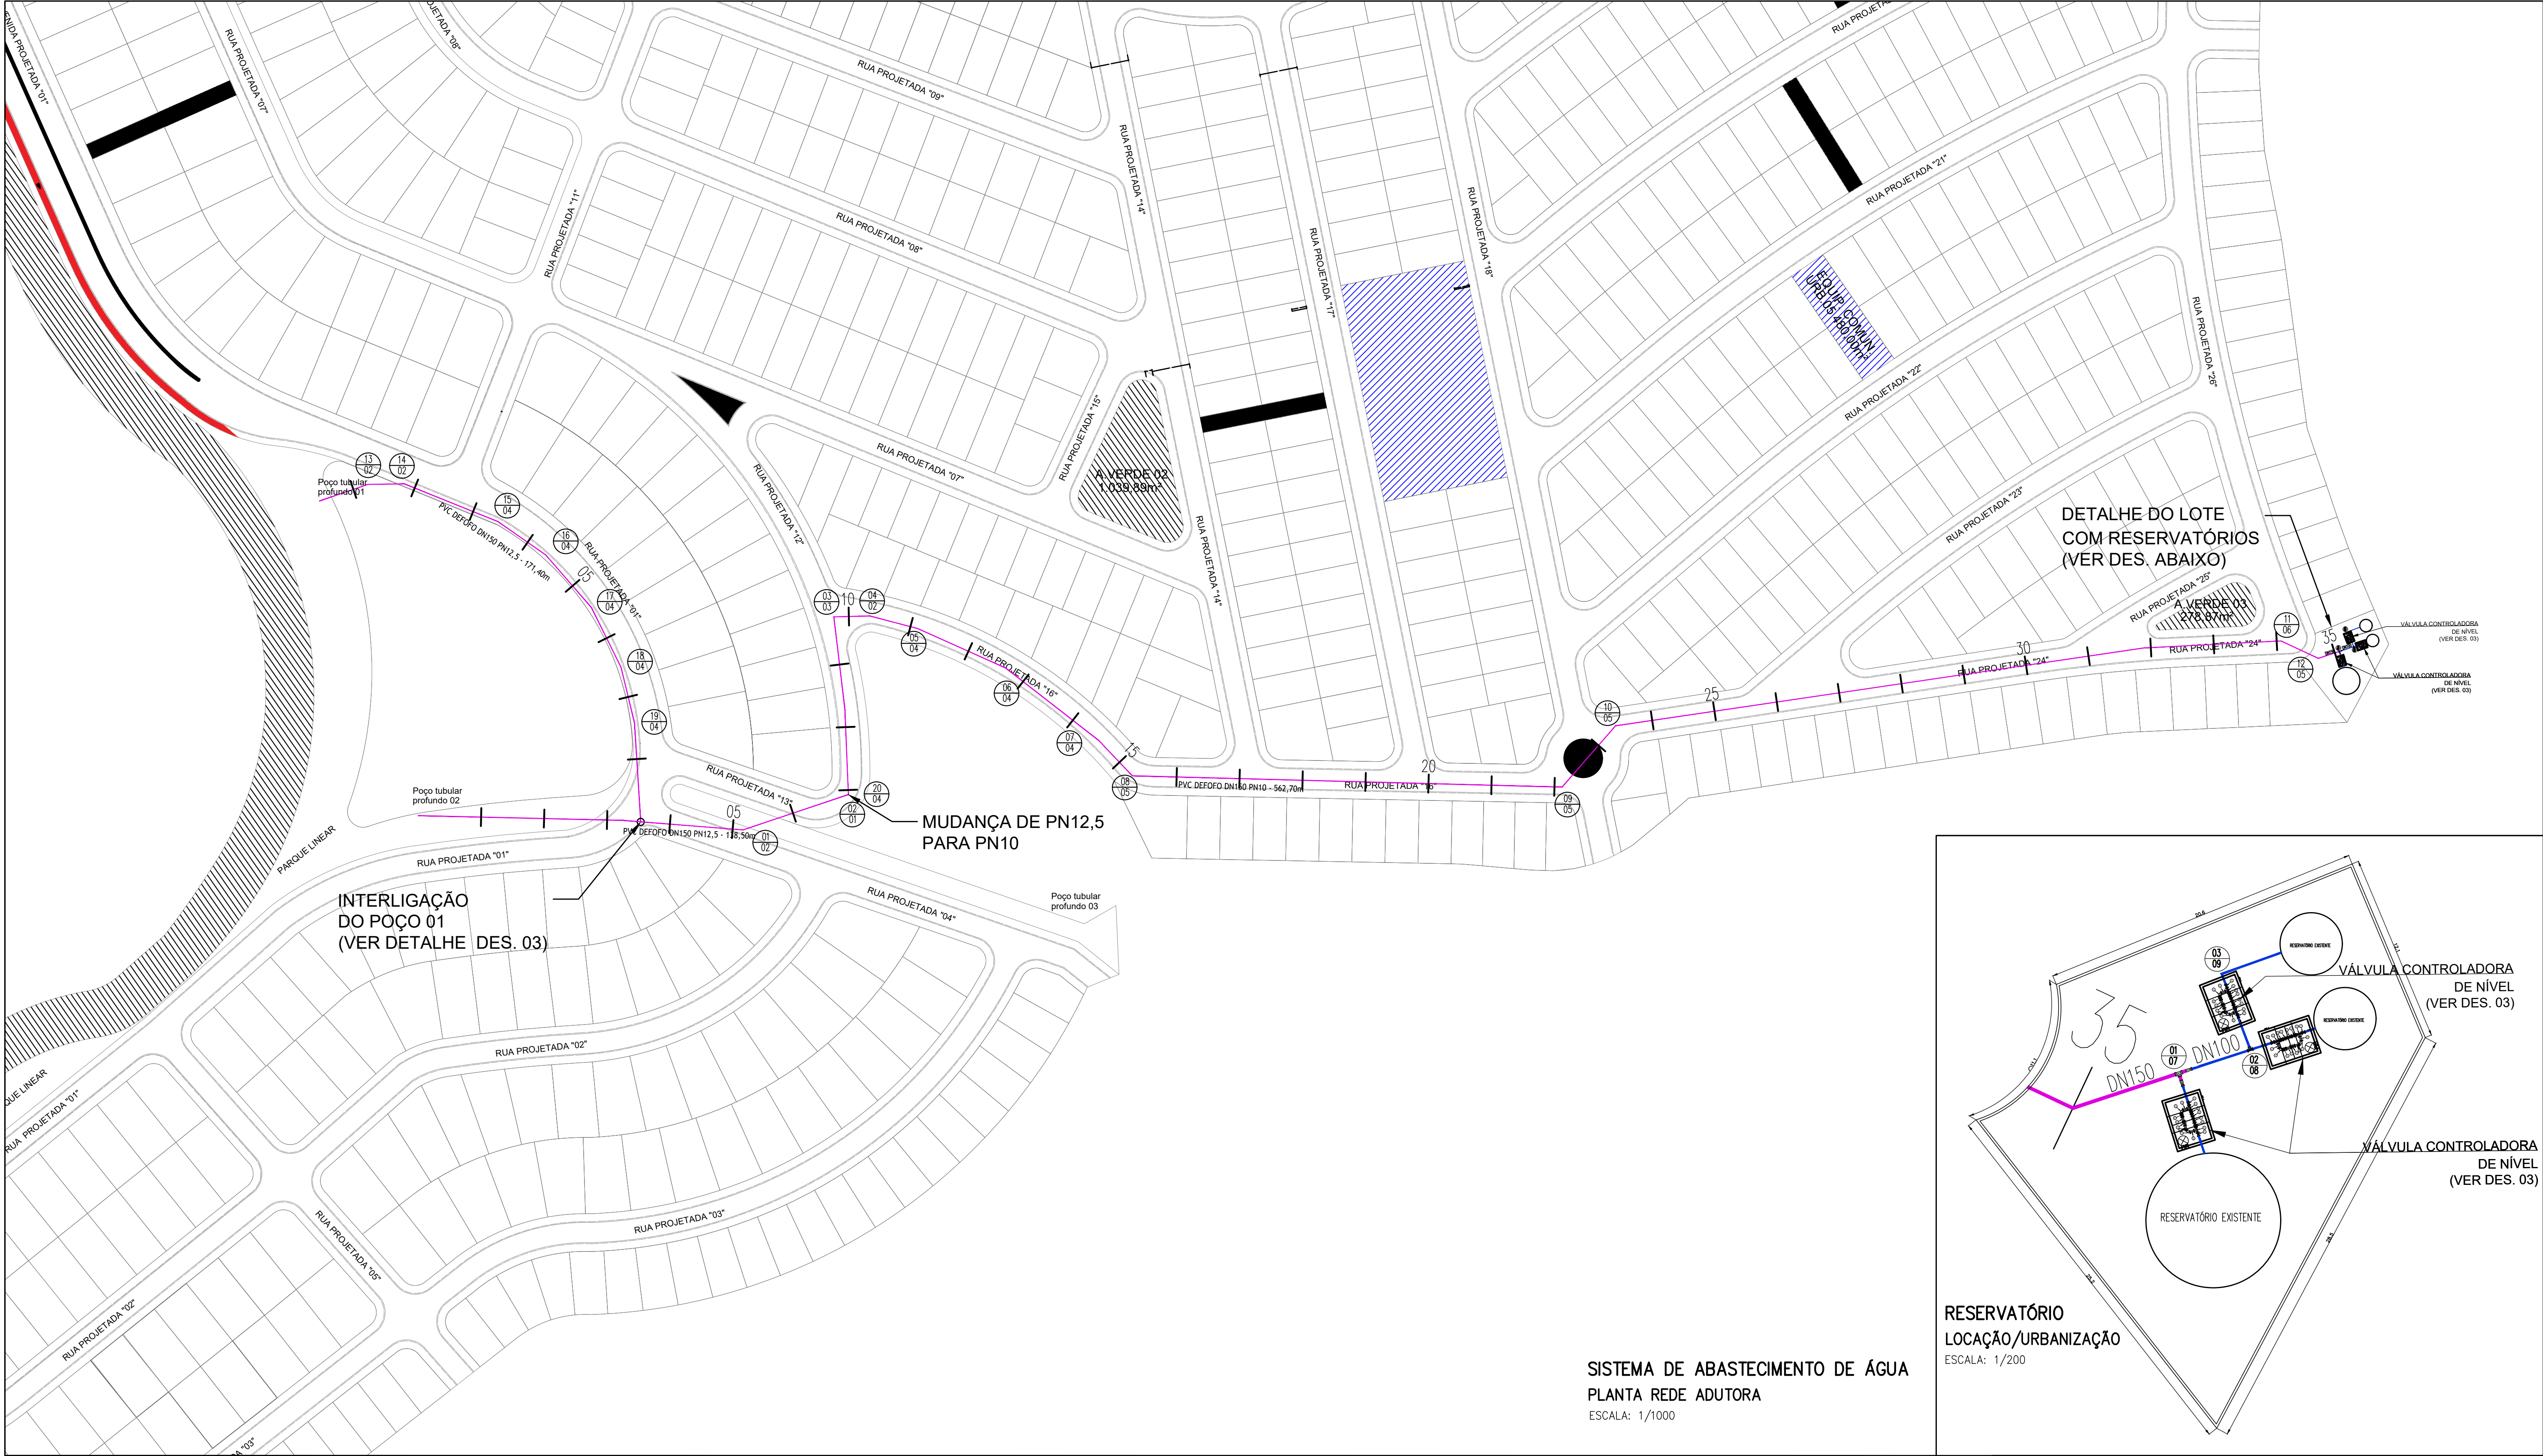

DETALHAMENTO DOS NÓS REDE ADUTORA

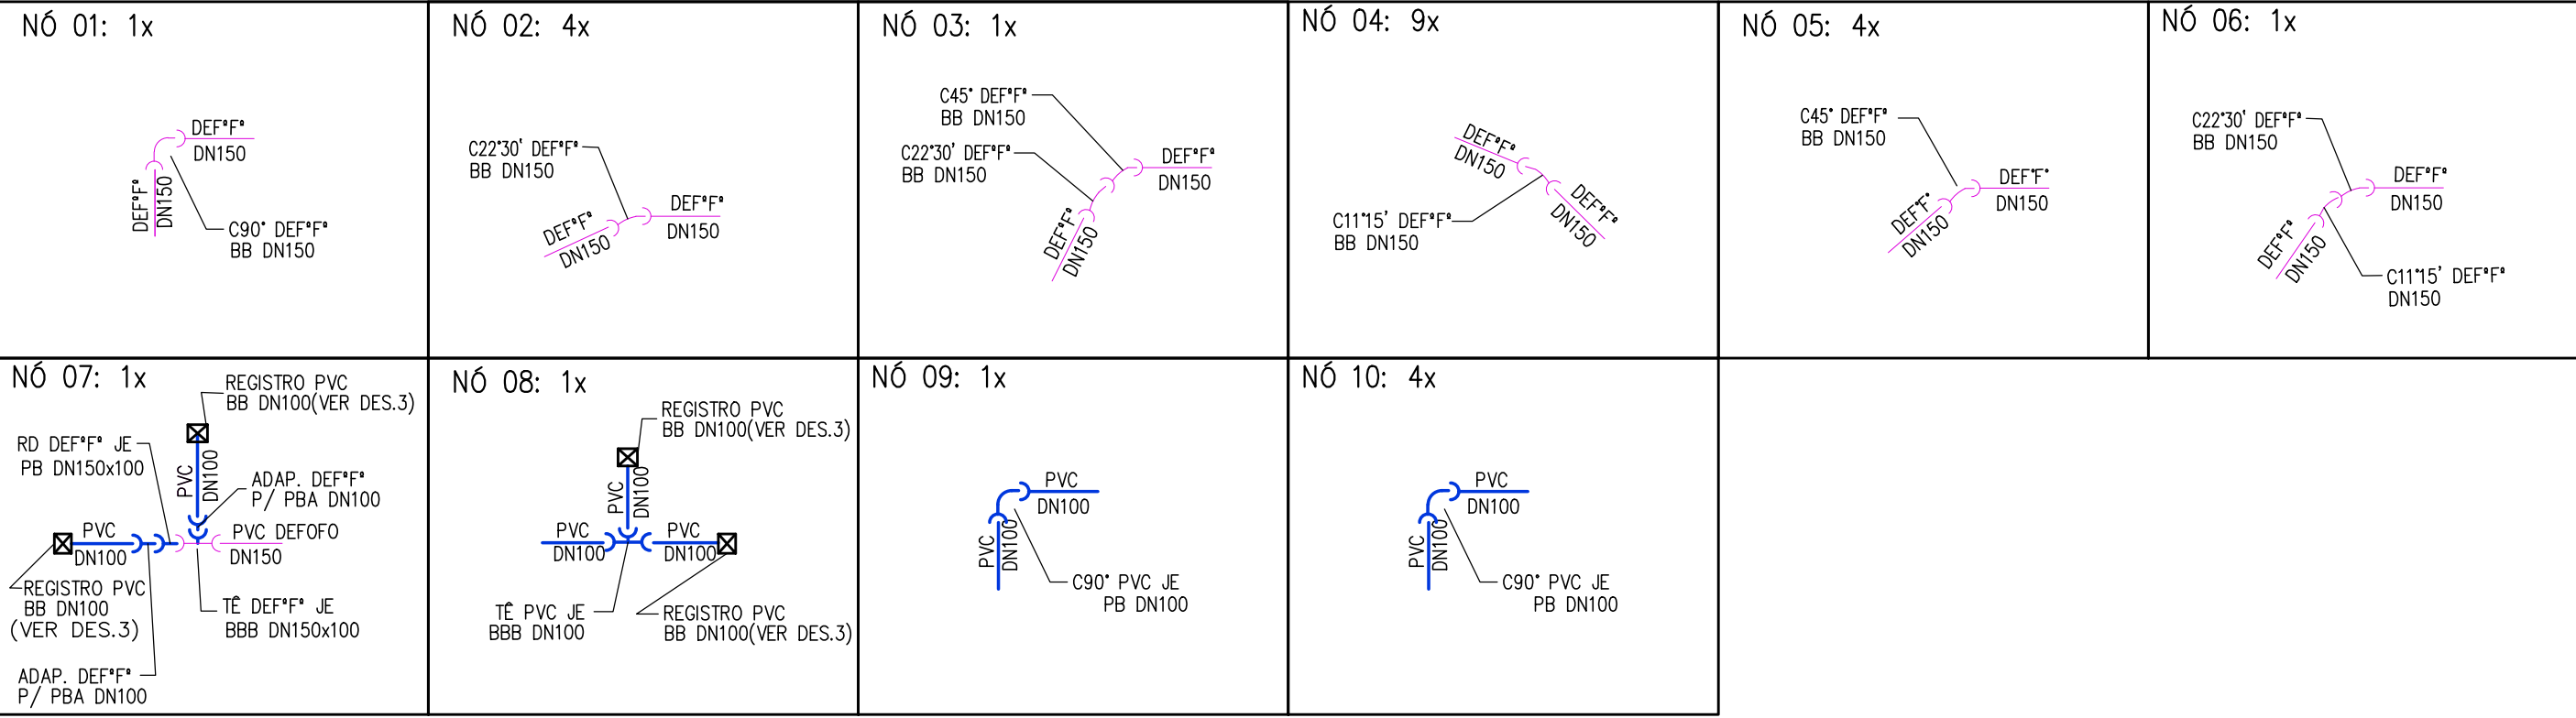

SISTEMA DE ABASTECIMENTO DE ÁGUA PLANTA REDE ADUTORA

ESCALA: 1/1000

RELAÇÃO DE MATERIAL				
ÍTEM	DESCRIÇÃO	DN	QUANT.	UNID.
REDE ADUTORA				
1	CURVA DEF** BB 1115'	150	10	PÇ
2	CURVA DEF** BB 22'30"	150	06	PÇ
3	CURVA DEF** BB 45"	150	05	PÇ
4	CURVA DEF** BB 90"	150	01	PÇ
5	TE DEF** BBB	150X100	01	PÇ
6	TE PVC JE BBB	100	01	PÇ
7	CURVA PVC JE PB 90"	100	01	PÇ
8	REDUÇÃO PVC JE PB	150X100	02	PÇ
9	ADAPTADOR DEF** P/ PBA	100	02	PÇ
10	TUBO DEF** PB JE PN10 - L=6,00m	100	17,50	m
11	TUBO DEF** PB JE PN12,5 - L=6,00m	150	309,90	m
12	TUBO DEF** PB JE PN10 - L=6,00m	150	562,70	m

O	---	---	---	---
B	---	---	---	---
I	---	---	---	---
LETRA	DATA	ASSINATURA	DESCRIÇÃO	
REVISÕES				
 NOG Engenharia e Soluções em Saneamento LTDA Rua Alberto Cabral, 380A - Vila Pina Varginha-MG / (35) 3015-3044 RESPONSÁVEL TÉCNICO Eng. Felipe Pires Nogueira CREA: 256.818 COORDENADOR DA EMPRESA PROJETISTA Eng. Felipe Pires Nogueira CREA: 256.818 PROJETISTA Felipe P. Nogueira CREA: 256.818			CONTRATO	ART
PROJETO			MIRANTE DO LAGO	
DATA			JULHO/2025	
ESCALA			INDICADAS	
TIPO			BS	
FOLHA			01/03	
APPROVADO			VISTO	
VISTO			VISTO	
VISTO			VISTO	
BOCAIUVA — MG				