


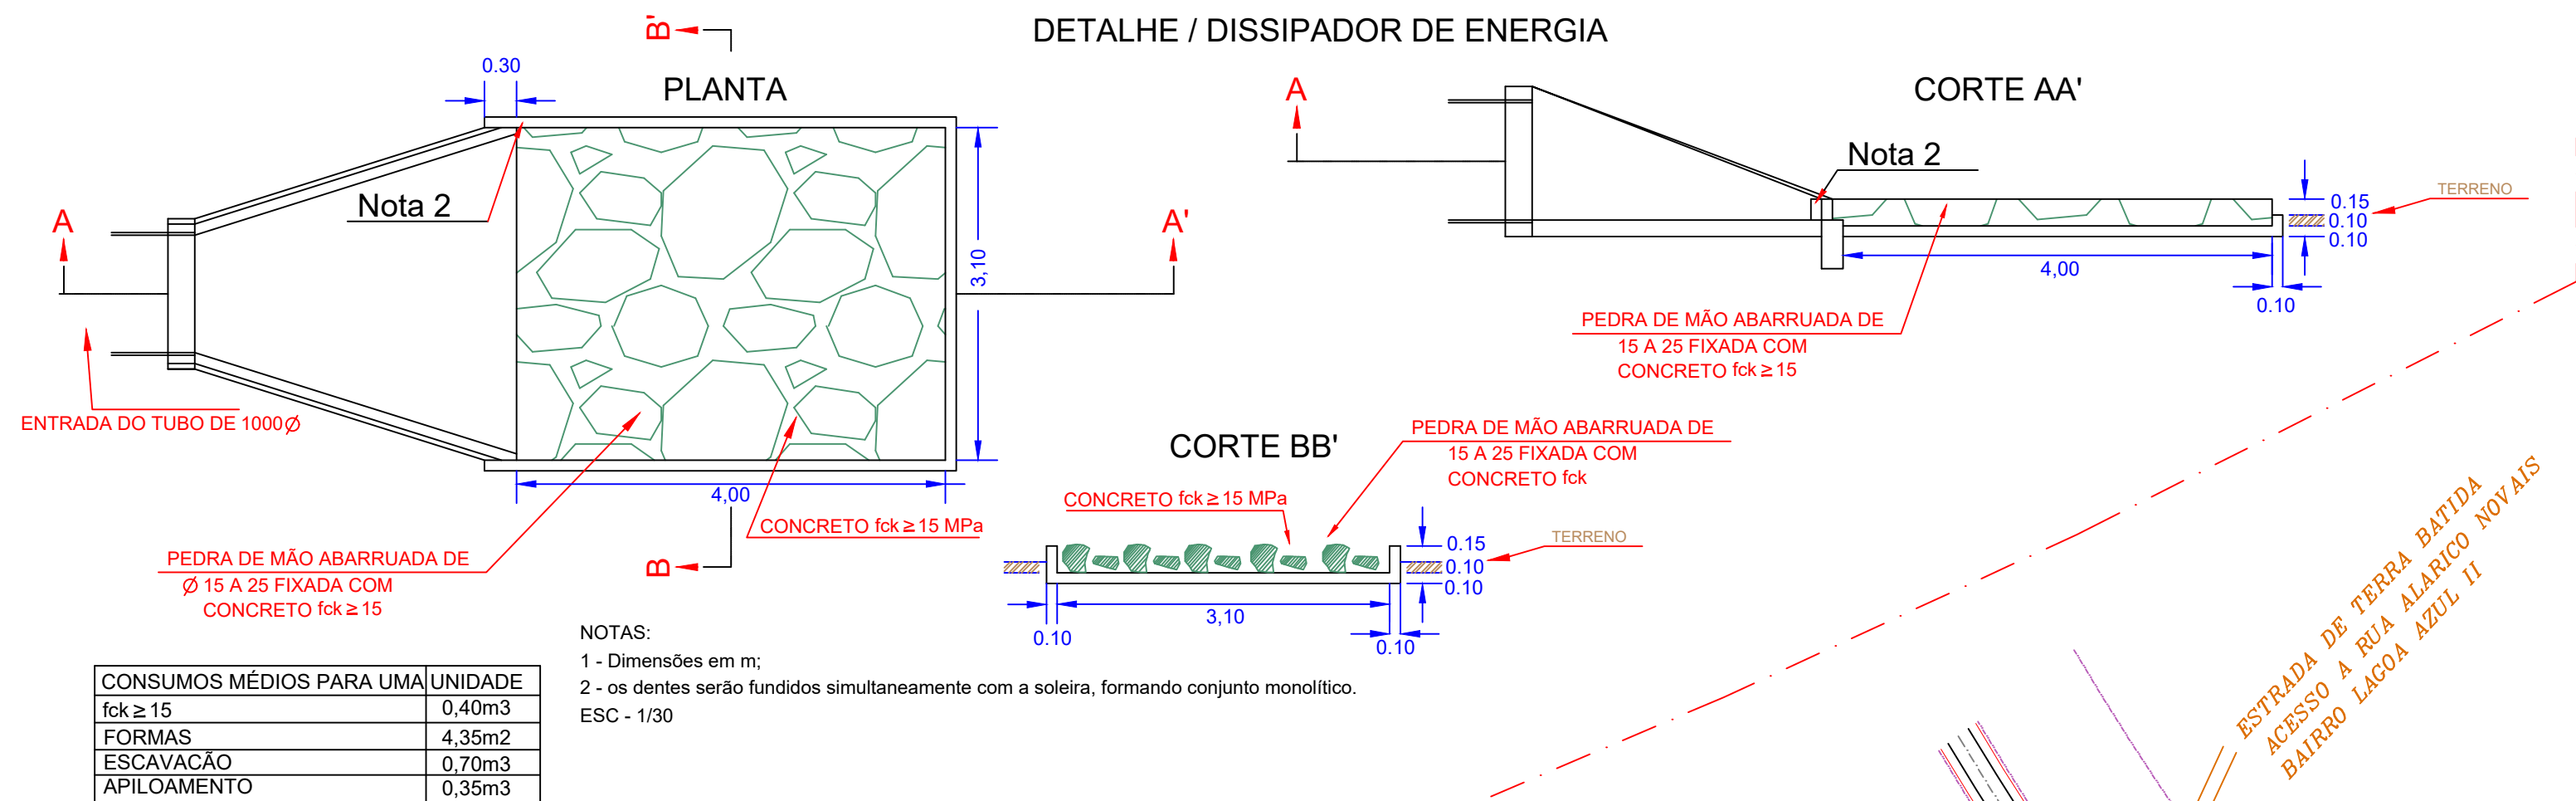

NOTAS TÉCNICAS:


- AS LIGAÇÕES ENTRE BOCAS DE LOBOS E POÇOS DE VISITA SERÃO EM TUBOS COM Ø0,40m.
- AS BOCAS DE LOBOS DEVEM SER SEMPRE EXECUTADAS DO MEIO DA TESTADA DO LOTE PARA A PARTE MAIS BAIXA DEIXANDO A PARTE SUPERIOR DA FRENTE DO LOTE PARA A FUTURA GARAGEM.
- BL= BOCA DE LOBO
- PV= POÇO DE VISITA
- CX= CAIXA DE RECEPÇÃO
- A TUBULAÇÃO EM TUBOS DE CONCRETO CLASSE C1 E CA2

LEGENDA

- A - DIÂMETRO DA TUBULAÇÃO (m)
- B - DECLIVIDADE DA TUBULAÇÃO (%)
- C - COMPRIMENTO DO TRECHO (m)
- D - PROFUNDIDADE DA TUBULAÇÃO (m)
- E - COTA DO TERRENO (m)
- F - COTA DE FUNDO DO PV OU CP
- G - PROFUNDIDADE DO PV OU CP
- PV - POÇO DE VISITA
- BL - BOCA DE LOBO SIMPLES
- SENTIDO DO FLUXO
- CP - CAIXA DE PASSAGEM



DISSIPADOR DE ENERGIA - VER DETALHE

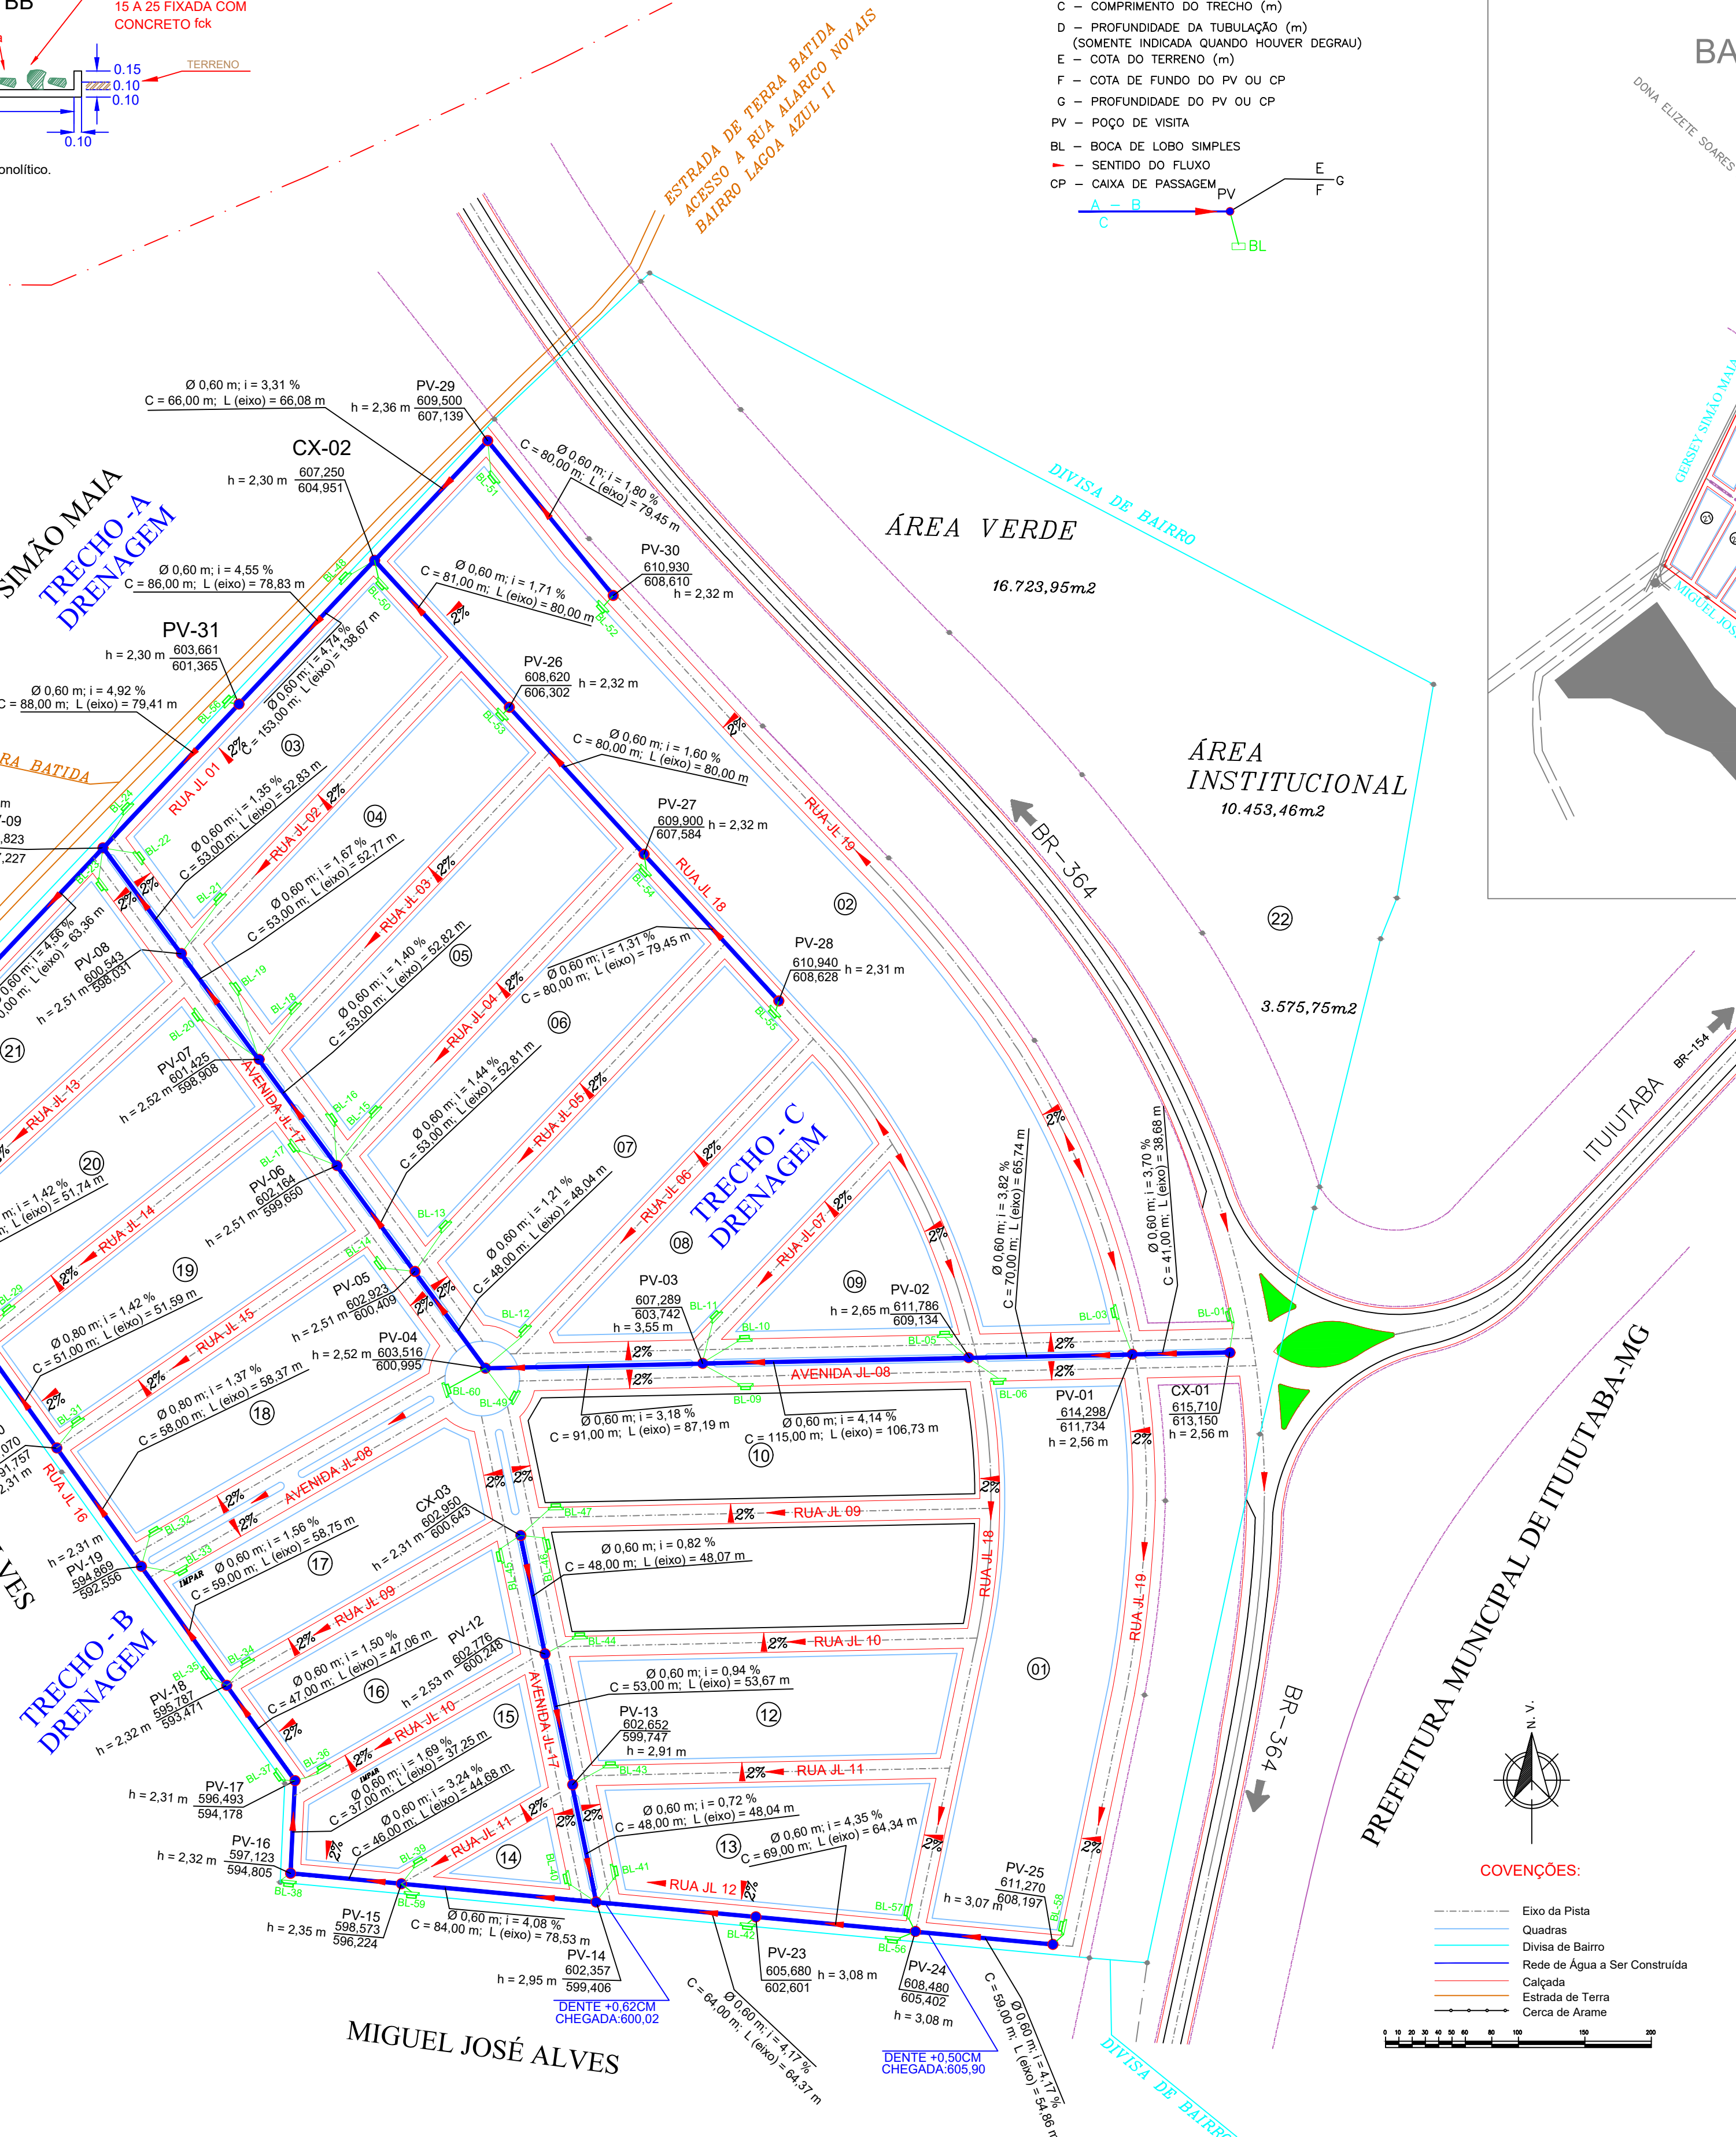

R&S ENGENHARIA LTDA
Rua Eurípedes da Silva Sales 339
São Francisco, Catalão - GO
CEP: 75707-260
(34) 99176-6327

Projeto de Drenagem

Identificação	Conteúdo Projeto da Rede de Água Pluviais		
	Local: Residencial Joaquim Leme Obs: Próximo ao Aeroporto Tito Teixeira		
	Cidade: Ituitaba - MG	Bairro: Residencial Joaquim Leme	
	Proprietário: C&A Construtora		
Desenho: Hagamenon	Escala: Indicadas	Conteúdo: Rede de Águas Pluviais	
Data: Julho/2016	Folha: 1/13	Aprovação:	
Assinaturas:		Aprovação:	
Proprietário: C&A Construtora		Resp. Técnico: Engº Civil: Clovis Moreira de Barros CREA - MG 75954/D Telef. : (64) 8112-9136 Email : contato@rsengenharia.net	