


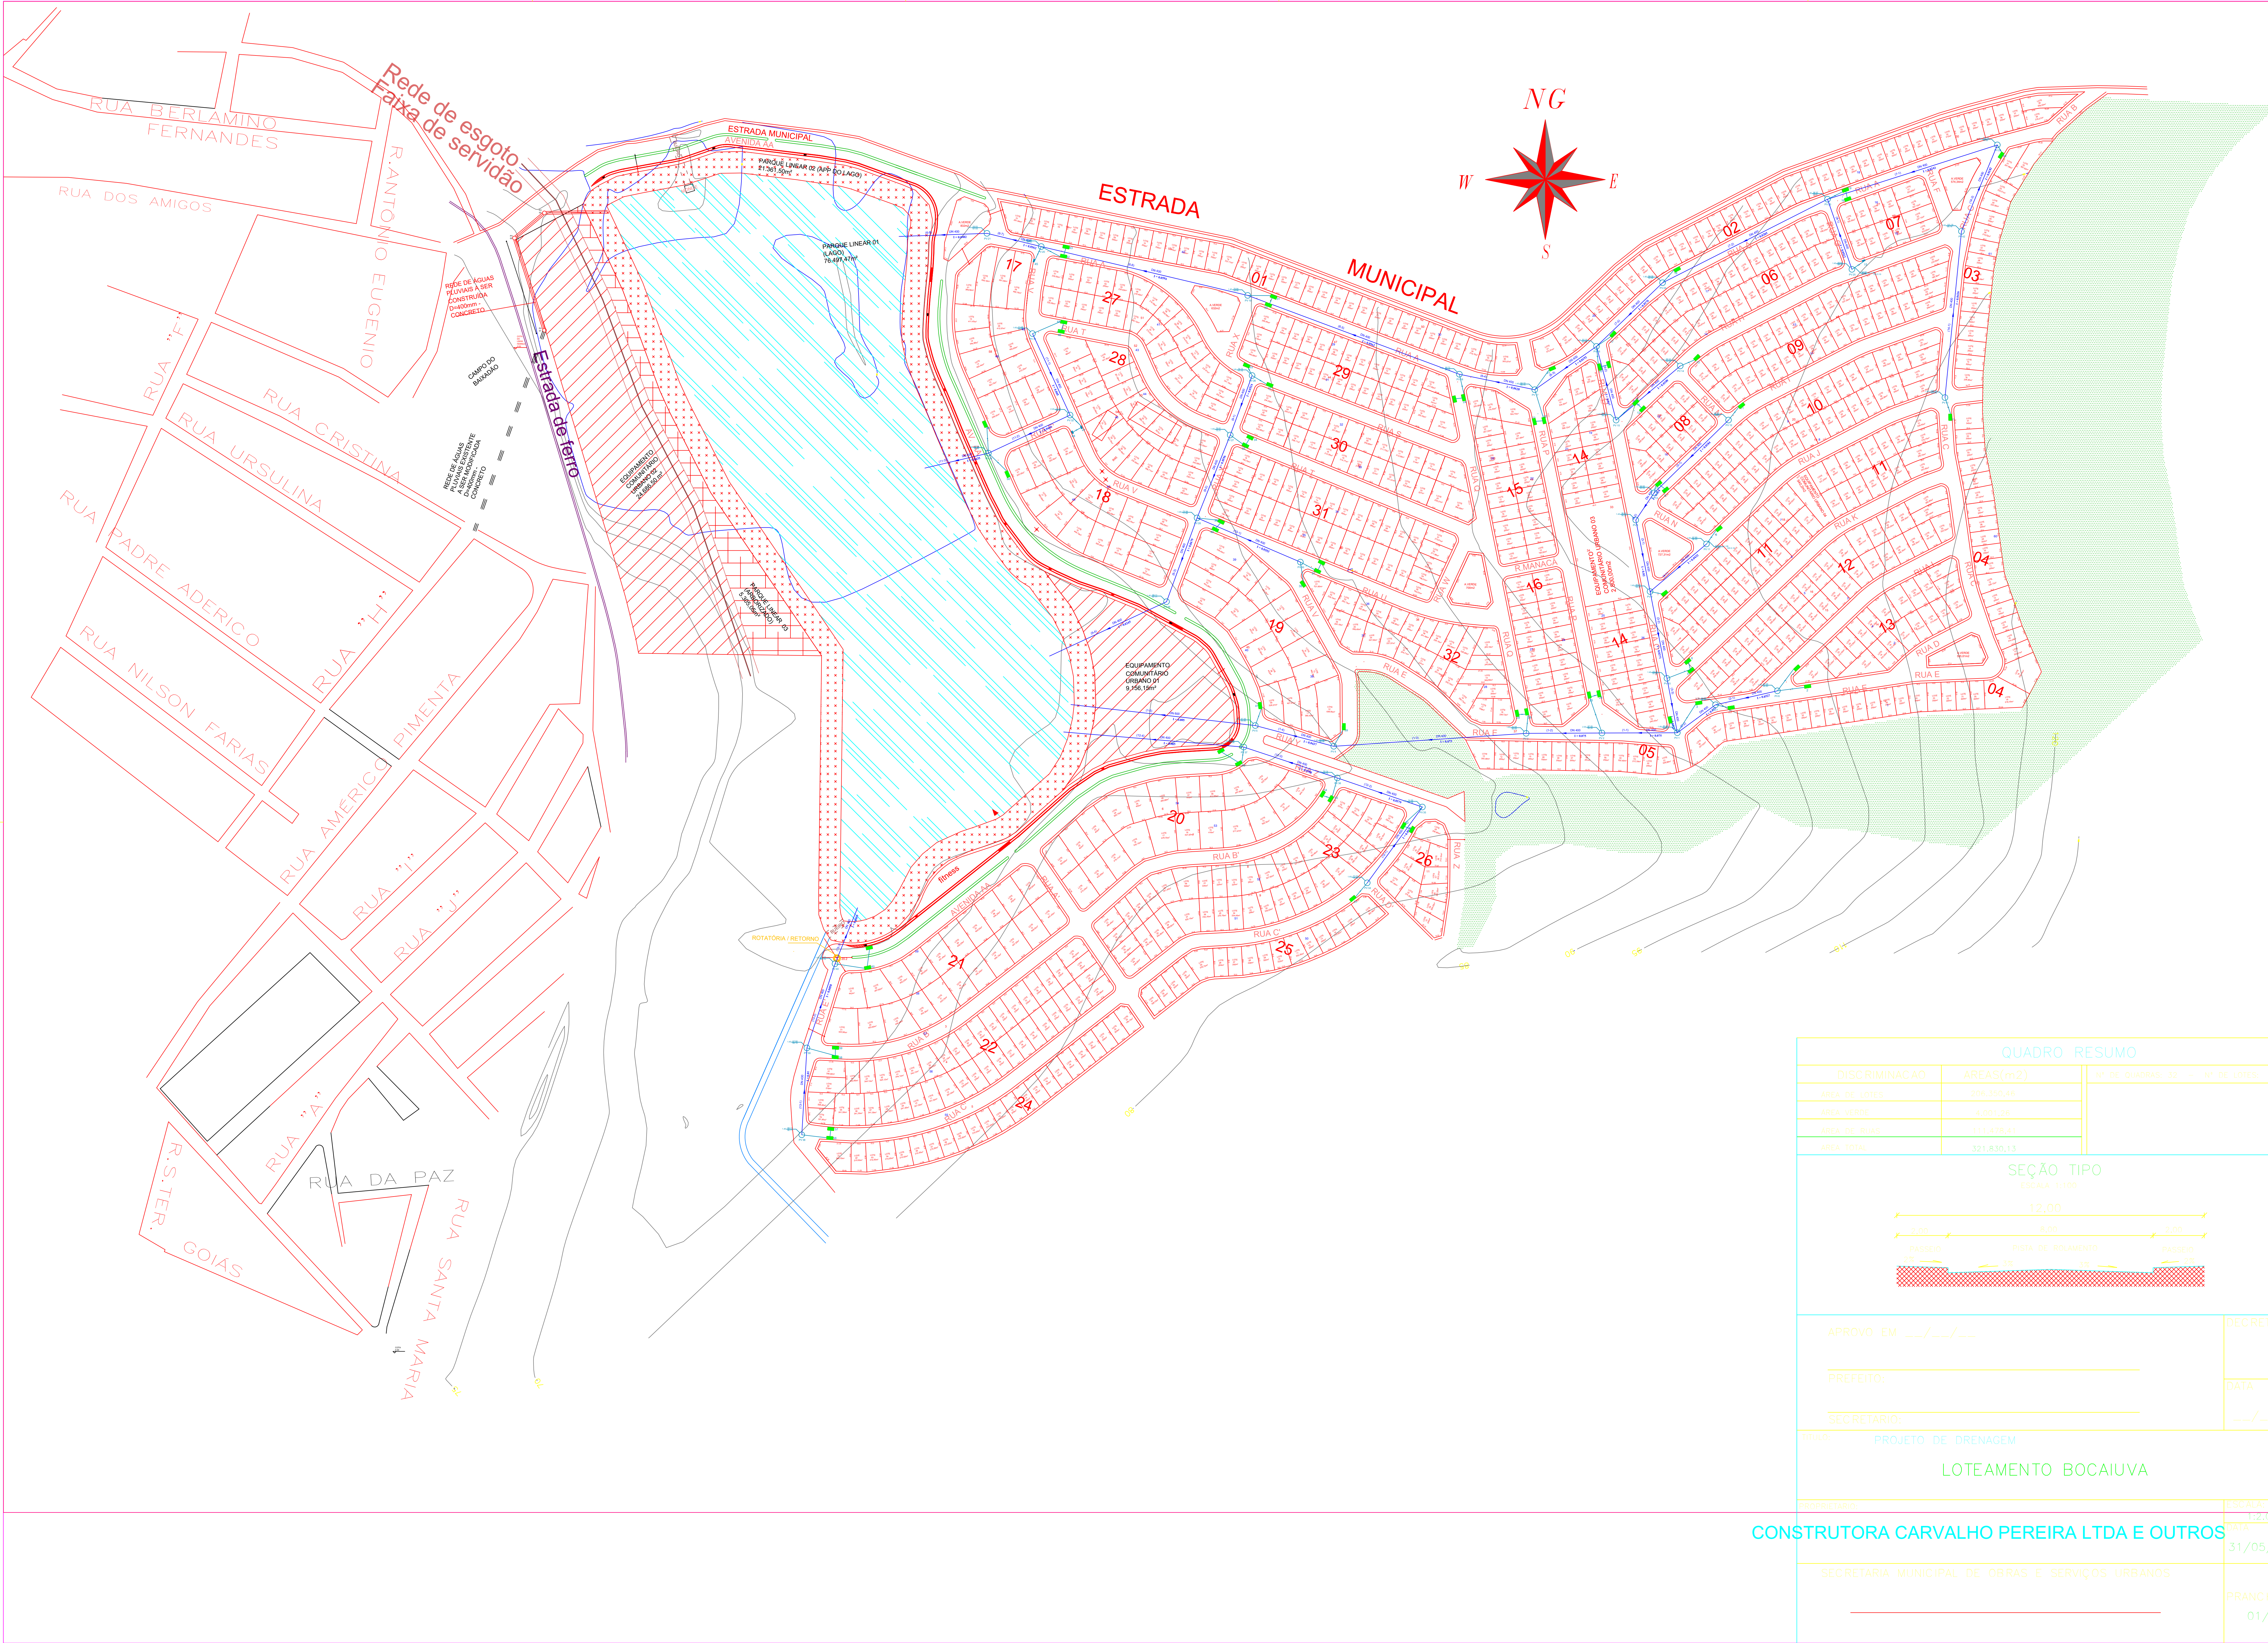

QUADRO RESUMO

DISCRIMINACAO	AREAS(m2)	NT DE QUADROS: 32	NT DE LOTES: 830
AREA DE LOTES	306.350,46		
AREA VERDE	4.001,09		
AREA DE RUAS	111.435,41		
AREA TOTAL	321.830,13		

SEÇÃO TIPO

ESCALA: 1:100

APROVO EM ____/____/____

PREFEITO: _____

SECRETARIO: _____

DECRETO Nº: _____

DATA: ____/____/____

TITULO: PROJETO DE DRENAGEM

LOTEAMENTO BOCAIUVA

CONSTRUTORA CARVALHO PEREIRA LTDA E OUTROS

SECRETARIA MUNICIPAL DE OBRAS E SERVIÇOS URBANOS

ESCALA: 1:2.000

DATA: 31/05/2015

PRANCHA Nº: 01/01