


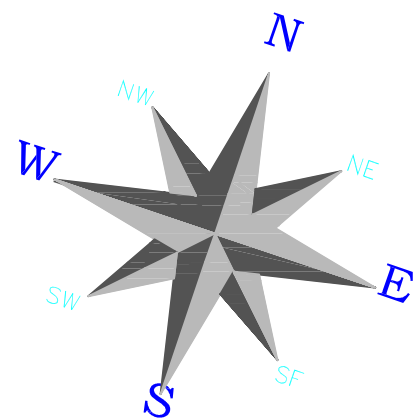

CEMIG	Data	NS
	01/06/22	1139847257
Esta liberação não isenta a empreiteira quanto a observância das normas e padrões da CEMIG D e eventuais falhas no projeto não reconhecíveis na análise		
Liberado por: Lucas Giovanni de Carvalho Rocha		
EM/PE Nº. Pessoal: E248846		

PROJETO ELABORADO DE ACORDO COM AS ESPECIFICAÇÕES DA OM/PE, OM/EX E PE/OS. PRÉ-ANÁLISE ARQUIVADA.

Lucas Giovanni de Carvalho Rocha
Conferido por: EM/PE Nº. Pessoal: E248846

LEGENDA	
90LD	LUMINÁRIA 90W-LED EM BRAÇO DO TIPO MÉDIO
120LD	LUMINÁRIA 190W-LED EM BRAÇO DO TIPO MÉDIO


A

B

Características Transformador
Nº da Cia
Fabricante
Nº da Série
Entregue
Obs:

Características Transformador
Nº da Cia
Fabricante
Nº da Série
Entregue
Obs:

CÁLCULOS DE ESFORÇOS

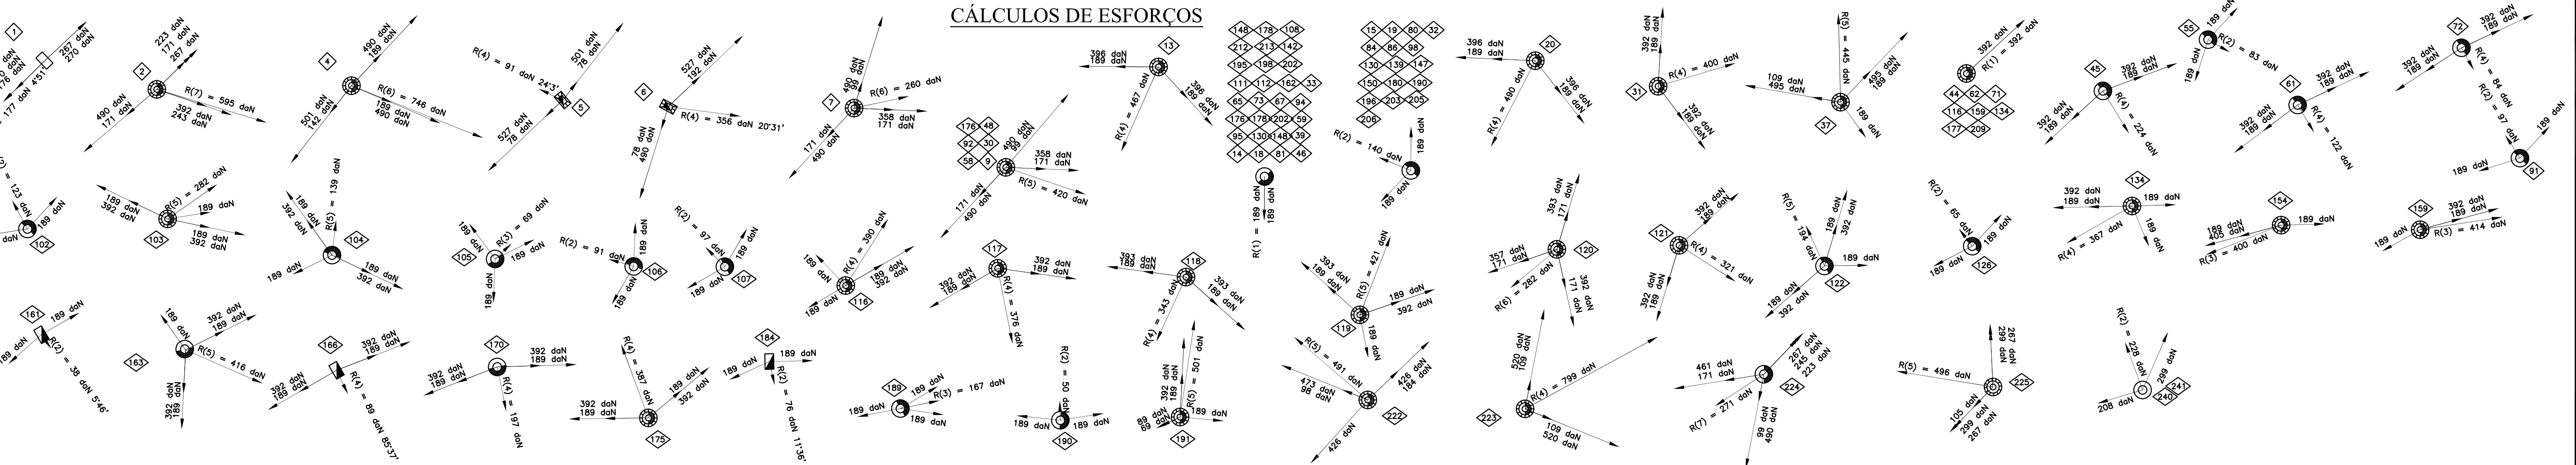

- NOTAS:
- OS CONDUTORES DE BAIXA TENSÃO NÃO ESPECIFICADOS SÃO MULTIPLEX 3x1x70+37
 - OS BRAÇOS DE L.P. A SEREM UTILIZADOS SERÃO DO TIPO MÉDIO.
 - MÉDIO FIO EXISTENTE.
 - PROJETO SEM IMPACTO AMBIENTAL.
 - OS POSTES PROJETADOS E NÃO ESPECIFICADOS SÃO DE 11m 300daN
 - AS ESTRUTURAS DE MÉDIA TENSÃO PROJETADAS E NÃO ESPECIFICADAS SÃO DO TIPO "CEI".
 - TODOS POSTES DE 11m 300daN A SEREM INSTALADOS DEVERÃO SER ENGASTADOS COM PROFUNDIDADE AUMENTADA (PA) DE 1,20m.
 - TODOS OS POSTES DE 600daN COM SIMBOLOGIA DE BASE CONCRETADA, DEVERÃO SER COM DIÂMETRO INDICADO NA TABELA D POSTES COM PROFUNDIDADE AUMENTADA OU BASE CONCRETADA (AO LADO).
 - OS POSTES COM SIMBOLOGIA "PA" (PROFUNDIDADE AUMENTADA), DEVERÃO SER ENGASTADOS CONFORME INDICADO NA TABELA D POSTES COM PROFUNDIDADE AUMENTADA OU BASE CONCRETADA (AO LADO).
 - NO POSTE Nº. 28, DEVERÁ ABAIXAR A B.T. EM 0,150mm E SUBIR A M.T. EM 0,100mm.
 - OS CONDUTORES DE MÉDIA TENSÃO 3/50+9,5 E 3/150+95 SÃO EM 13,8kV.

RESISTÊNCIA DO POSTE (daN)	PA-PROFUNDIDADE AUMENTADA	BASE CONCRETADA
300	1,80m	NÃO
600	NÃO	Ø 0,90m
1000	NÃO	Ø 1,30m

PROJ.:
DATA: 14/04/2022

VISTO:
APROV.:
DATA:

RIBEIRO BARROSO
CONSTRUTORES ELÉTRICAS LTDA.

MODIFICAÇÃO E EXTENSÃO DE RDU P/ ATENDER O SR. SKY CONSTRUÇÕES E EMPREENDIMENTOS ITUIUTABA SPE LTDA NO LOTEAMENTO RESIDENCIAL JOAQUIM LEME EM ITUIUTABA.

ESCALA= 1 : 1000

NS: 1139847257

FOLHA: 1 / 2

