


CONVENÇÕES

TUBO DE Ø 150mm


DESA DE BARRIO

PAISADO

QUADRA

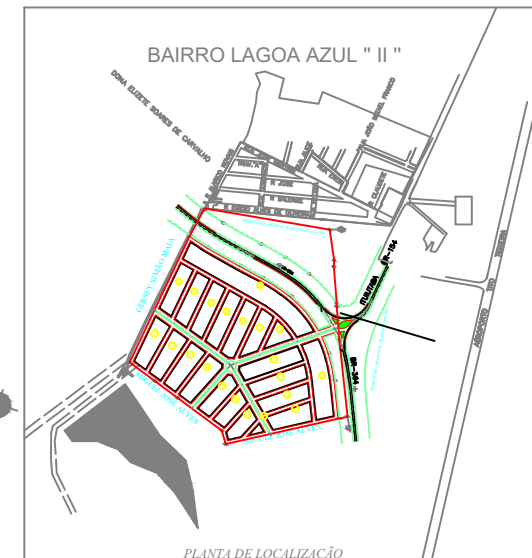

PLANTA DE LOCALIZAÇÃO

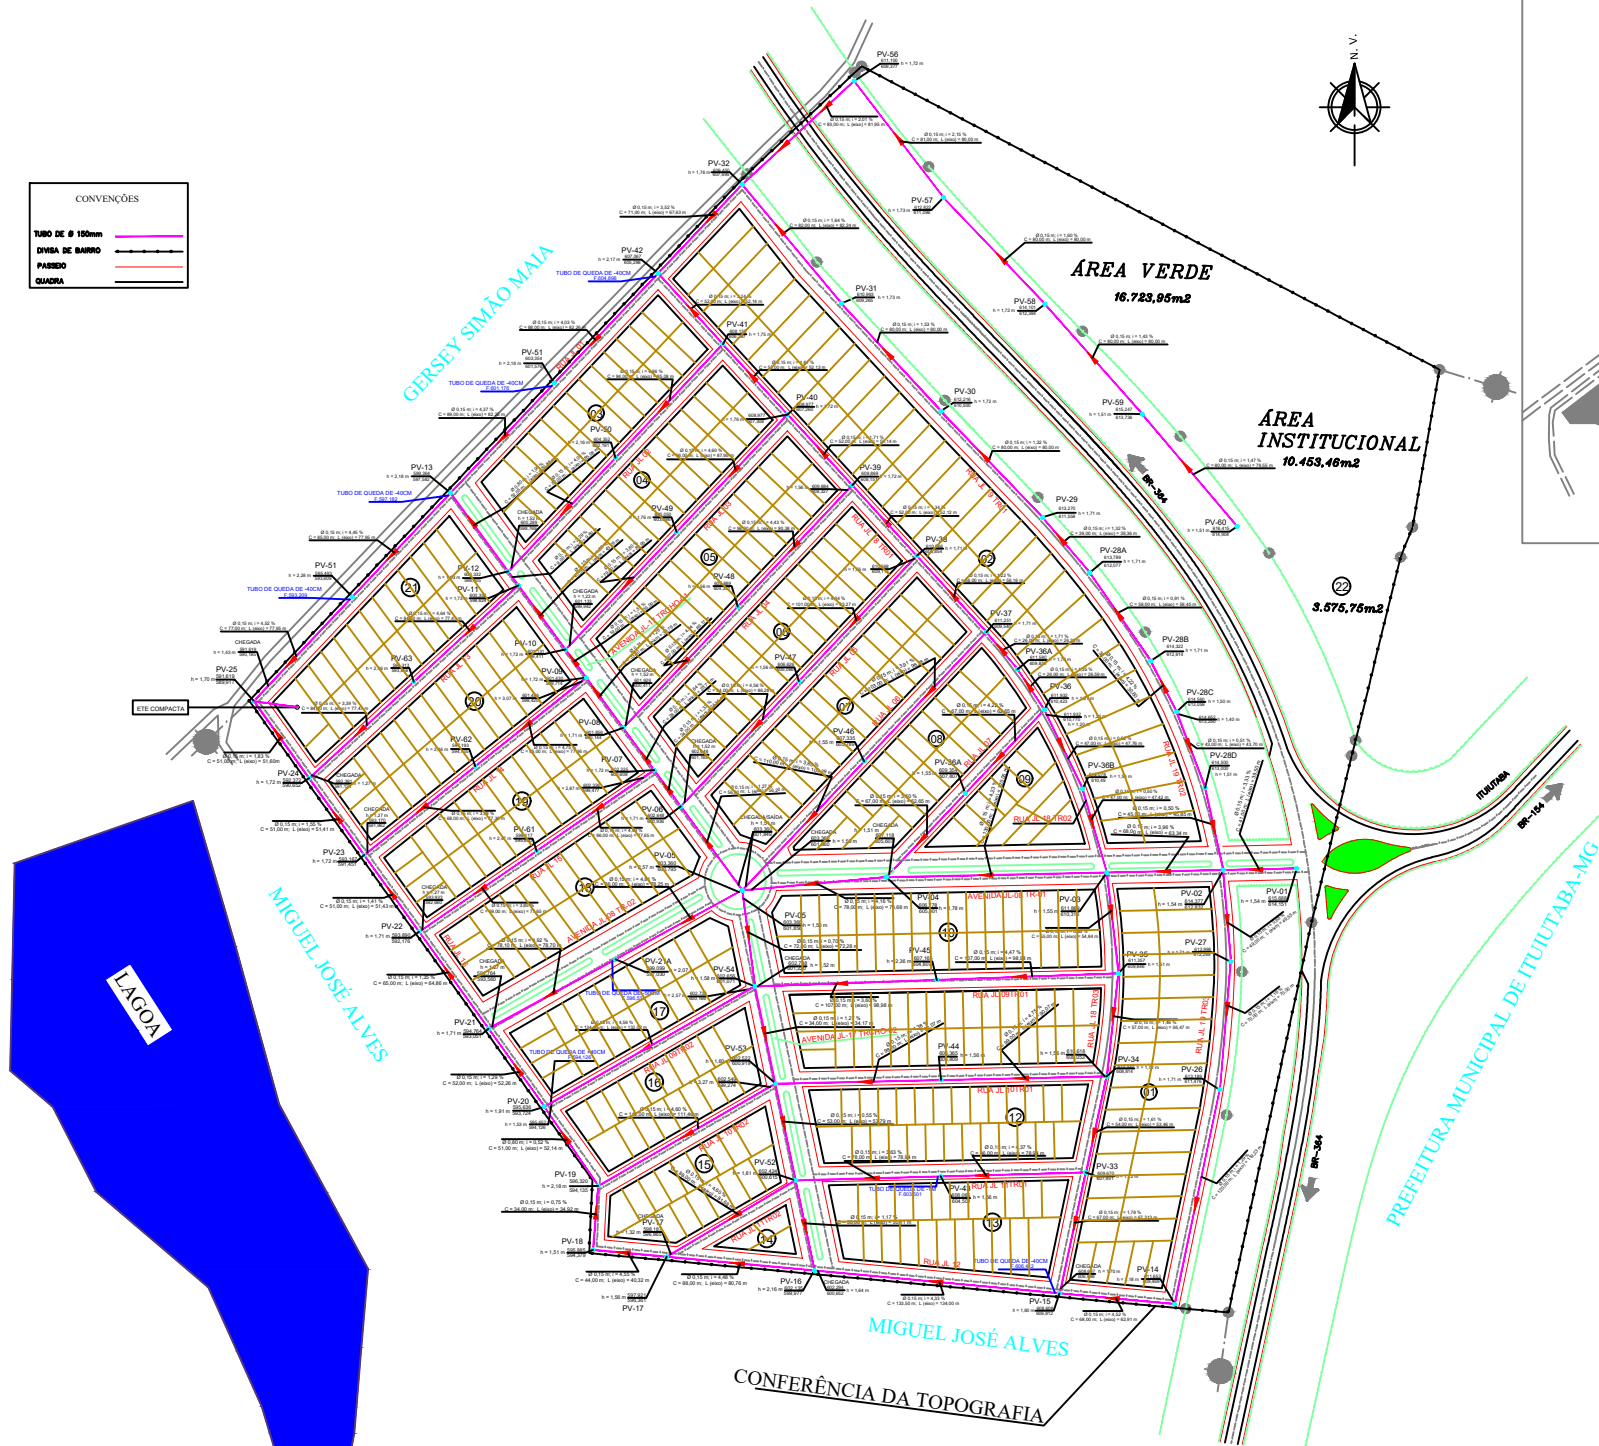

R&S ENGENHARIA LTDA
Rua Eurípedes da Silva Sales 339
São Francisco, Catalão - GO
CEP: 75707-260
(34) 99176-6327

Projeto de Esgoto

Identificação	Conteúdo	
	Projeto de Rede de Esgoto	
	Local:	Residencial Joaquim Lima
	Obras:	Próximo ao Aeroporto Tito Salazar
Proprietário	Cidade:	Ituituba - MG
	Bairro:	Residencial Joaquim Lima
Desenho:	Escalas:	Conteúdo:
	1:500	Rede de Esgoto
Data:	Folha:	18
	Setembro/2016	
Assinaturas:		Aprovação:
Proprietário:		
R&S Engenharia		
Revisão:		
Eng. Civil: Cláudio Moreira de Barros		
CREA: MG 199640		
Título: (34) 99176-6327		
Email: contato@rsengenharia.net		