


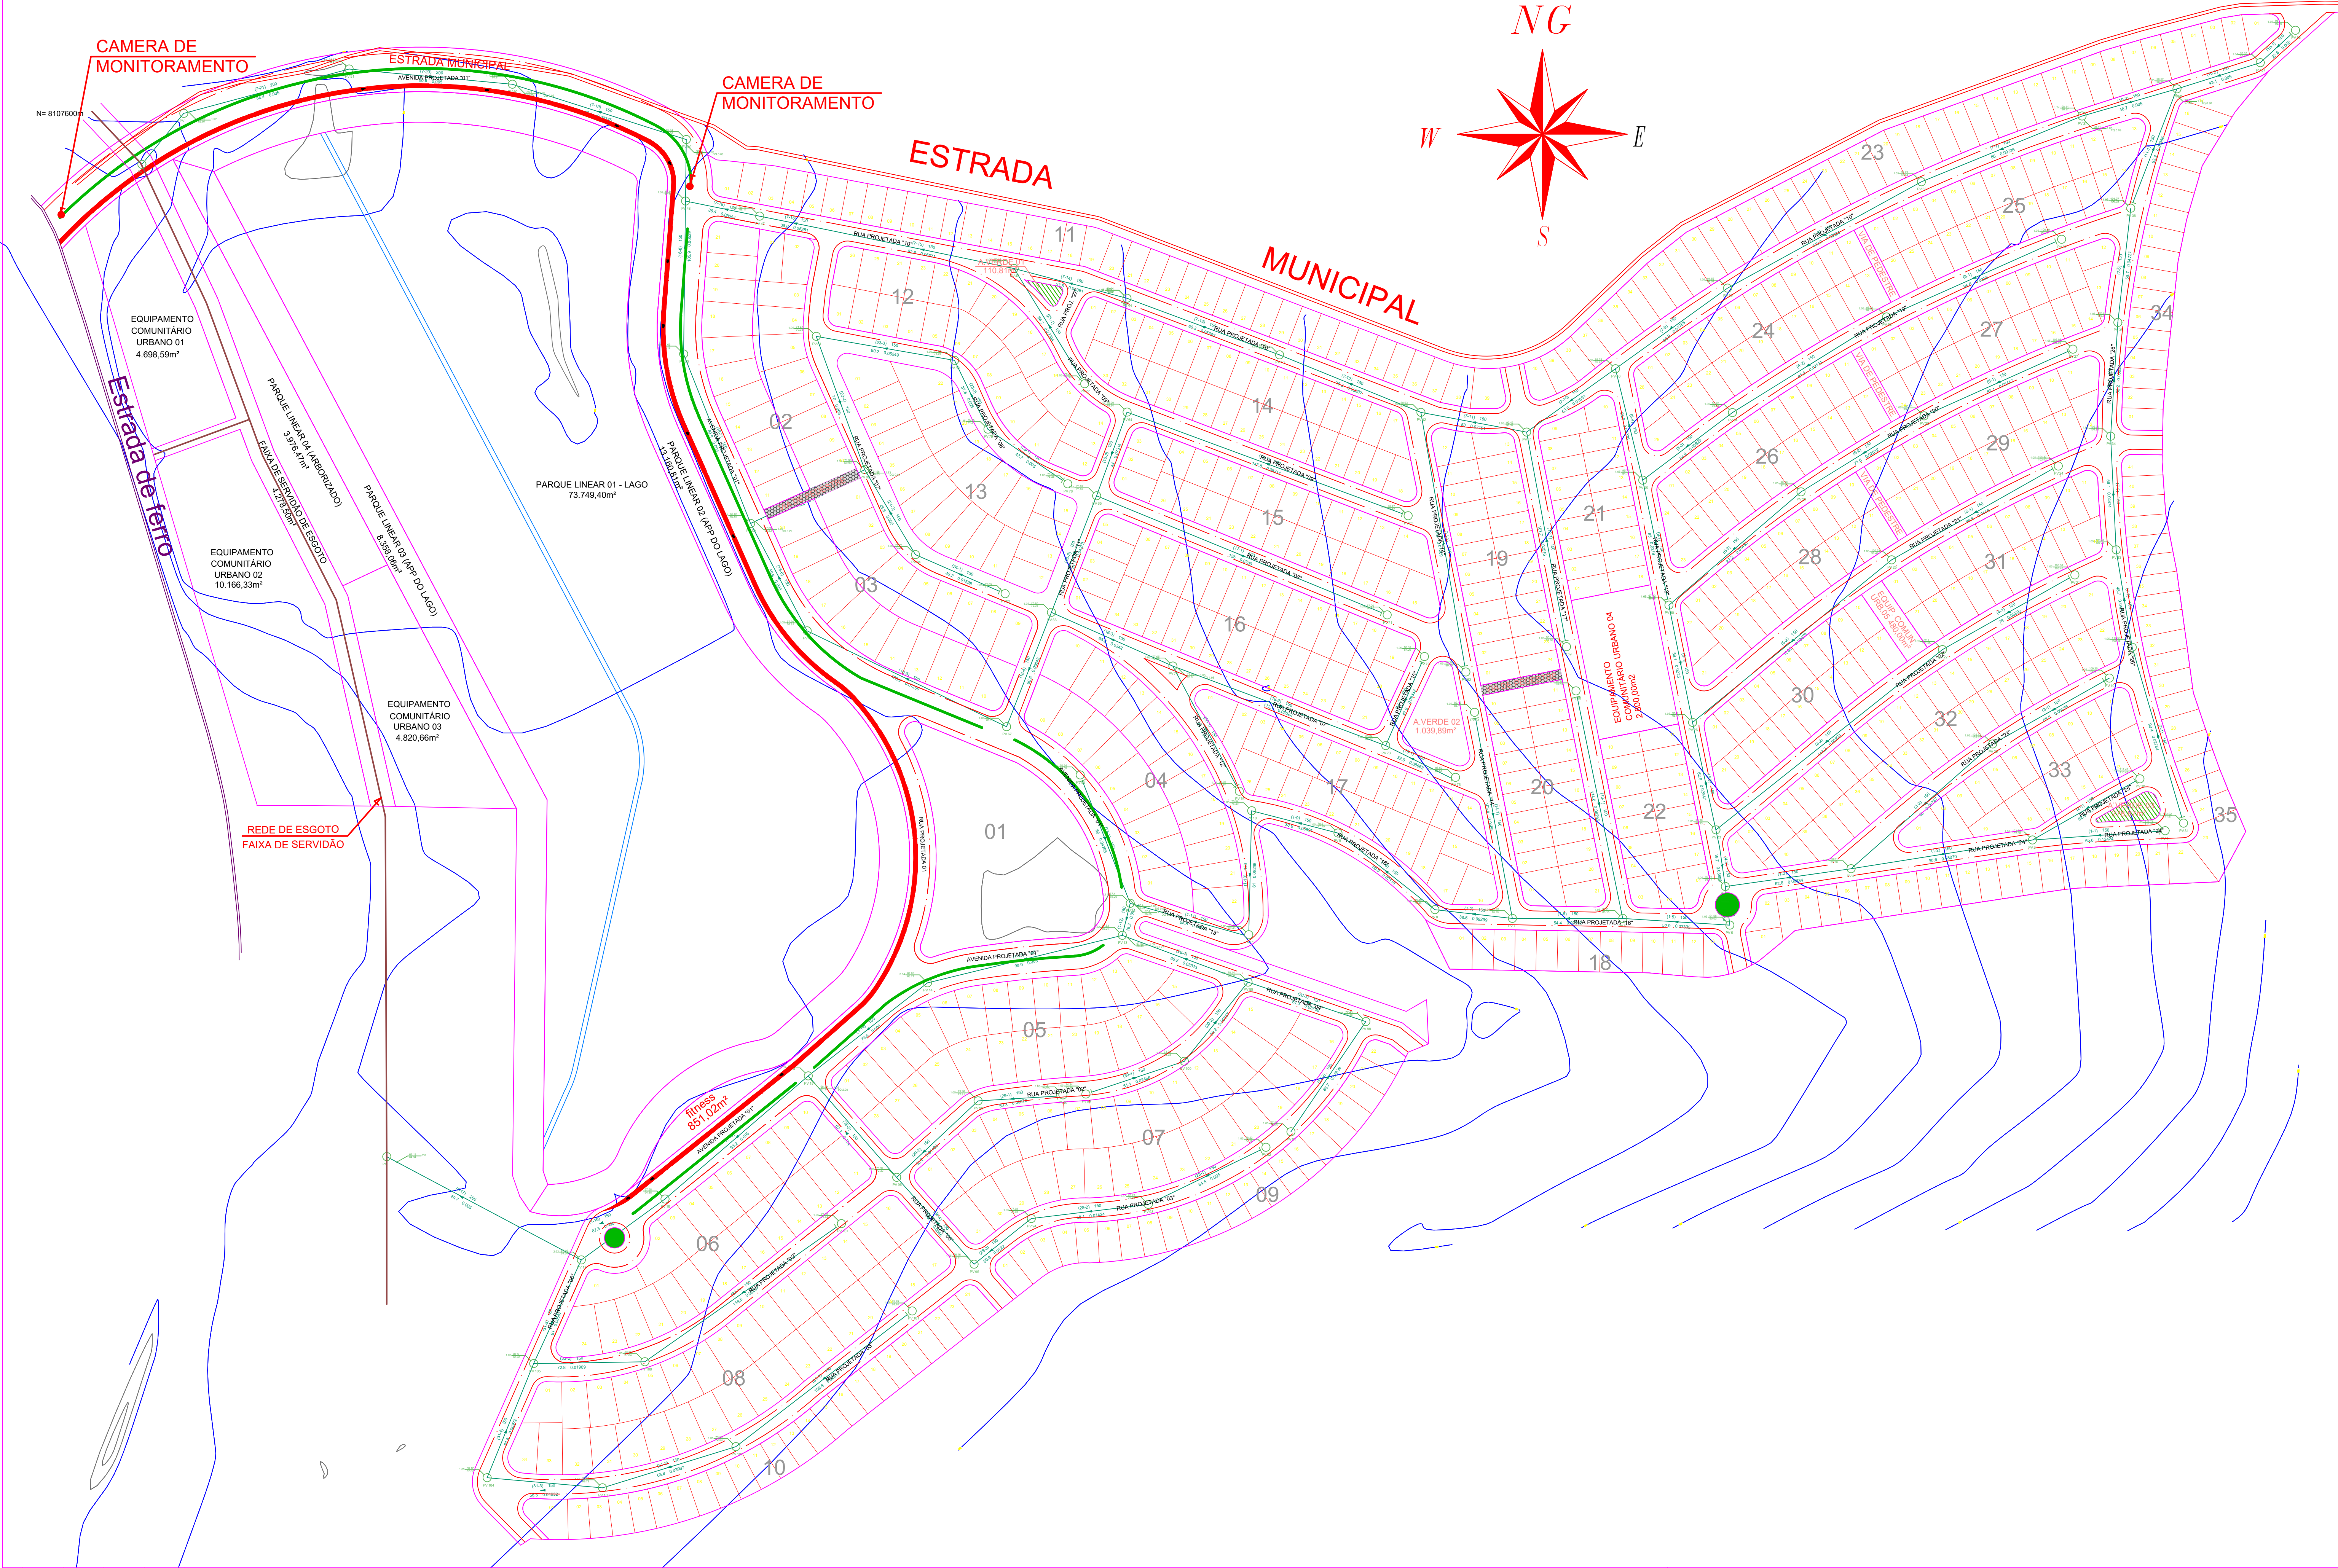

A				
B				
C				
	DATA	REVISÃO	PROJETO	APPROV
ALTERAÇÕES				

NOTAS:

TODA A REDE PROJETADA DEVE SER CONSTRUÍDA, MONITORADA, MANUTIDA E REPARADA DE ACORDO COM O NÍVEL DE SERVIÇO DE 100% DE CONFIABILIDADE.

LEGENDA:

PROJEÇÃO: UTM

PROJEÇÃO: UTM

PROJEÇÃO: UTM

PROJETO: ESGOTAMENTO SANITÁRIO LOTEAMENTO MIRANTE DA LAGOA

PROJETO: BOCALVA EMPREENDIMENTOS IMOBILIÁRIOS LTDA

PROJETO: ENGENHARIA HENRIQUE NASCIMENTO REIS

PROJETO: DATA: AGOSTO/2017

SAAE - SERVIÇO AUTÔNOMO DE ÁGUA E ESGOTO

BOCAIUVA - MG

SISTEMA DE ESGOTAMENTO SANITÁRIO

REDE DE COLETORES

LOTEAMENTO RESIDENCIAL BOCAIUVA

PLANTA CONSTRUTIVA

ESCALA: 1:1000

01

01 01