

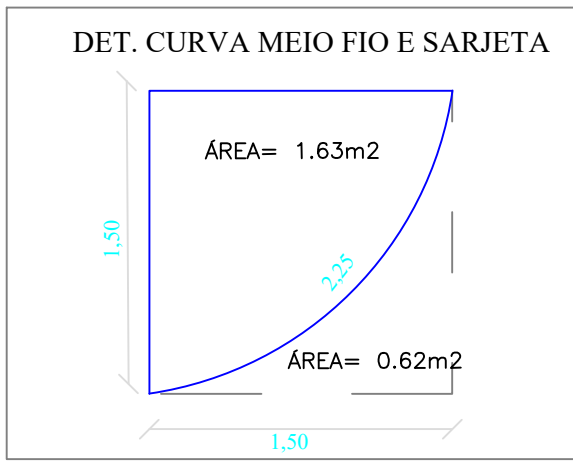


QUADRAS E SISTEMA VIÁRIO		
ESTUDO PRELIMINAR		
ESPECIFICAÇÃO	ÁREA (m2)	%
1- Áreas de Lotes Residencial Aberto (577 Lotes)	136.786,57	
2- Áreas Públicas	75.838,66	
2.1- Sistema Viário		
2.2- Espaços Livres de Uso Público		
2.3- Área Institucional	10.453,46	
3- Área Verde	16.723,95	
3.1- Faixa de Domínio	45.592,36	
4- Área Loteada	239.802,64	100,000
6- TOTAL DA GLEBA	285.395,00	100,000

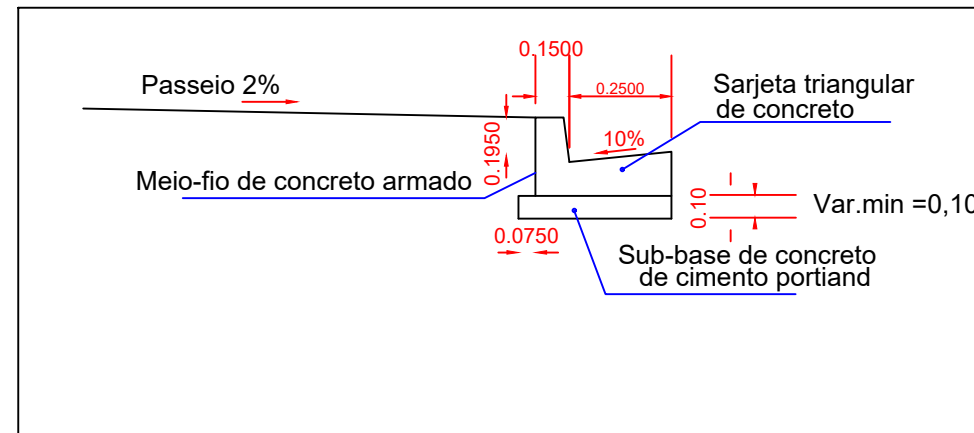




REVESTIMENTO (CBUQ) 0,025cm
BASE (BRITA) 0,15cm
SUB-BASE (BINDER) 0,10cm

ESC:1/30

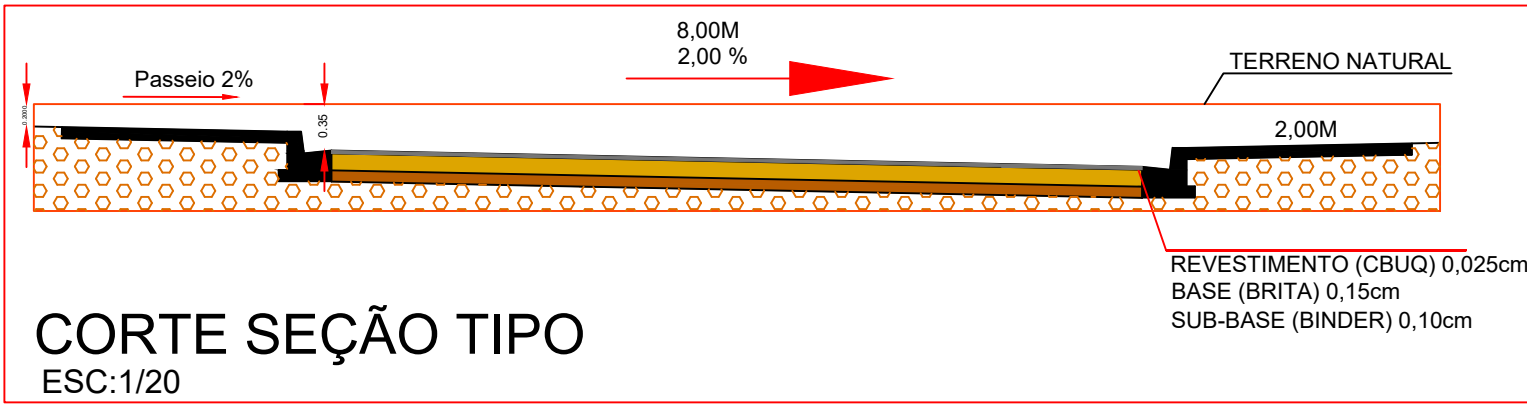

Quadro de Áreas

VIA	TRECHO	COMPRIMENTO(M)	L-PAVIMENTO(M)	LARGURA-TOTAL(M)	ÁREA-PAV	ÁREA-TOTAL
JL1	JL18 A JL16	390,51	7,5	8	3075,26625	3280,284
JL2	JL18 A AV-JL17	149,7	7,5	8	1178,8875	1257,48
JL3	JL18 A AV-JL17	156,33	7,5	8	1231,09875	1313,172
JL4	JL18 A AV-JL17	162,07	7,5	8	1276,30125	1361,388
JL5	JL18 A AV-JL17	168,22	7,5	8	1324,7325	1413,048
JL6	JL18 A AV-JL17	153,62	7,5	8	1209,7575	1290,408
JL7	AV-JL8 A JL18	108,4	7,5	8	853,65	910,56
AV-JL8	JL16 A JL19	456,77	15	16	7194,1275	7673,736
JL9	JL16 A JL18	294,01	7,5	8	2315,32875	2469,684
JL10	JL16 A JL18	261,24	7,5	8	2057,265	2194,416
JL11	JL12 A JL18	208,89	7,5	8	1645,00875	1754,676
JL12	JL16 A JL19	322,18	7,5	8	2537,1675	2706,312
JL13	JL16 A AV-JL17	144,02	7,5	8	1134,1575	1209,768
JL14	JL16 A AV-JL17	143,88	7,5	8	1133,055	1208,592
JL15	JL16 A AV-JL17	144,38	7,5	8	1136,9925	1212,792
JL16	JL01 A JL12	352,13	7,5	8	2773,02375	2957,892
AV-JL17	JL01 A JL12	444,94	15	16	7007,805	7474,992
JL18	JL01 A JL12	615,69	7,5	8	4848,55875	5171,796
JL19	JL01 A JL12	689,37	7,5	8	5428,78875	5790,708
		ÁREA TOTAL (M2)			49360,9725	52651,704

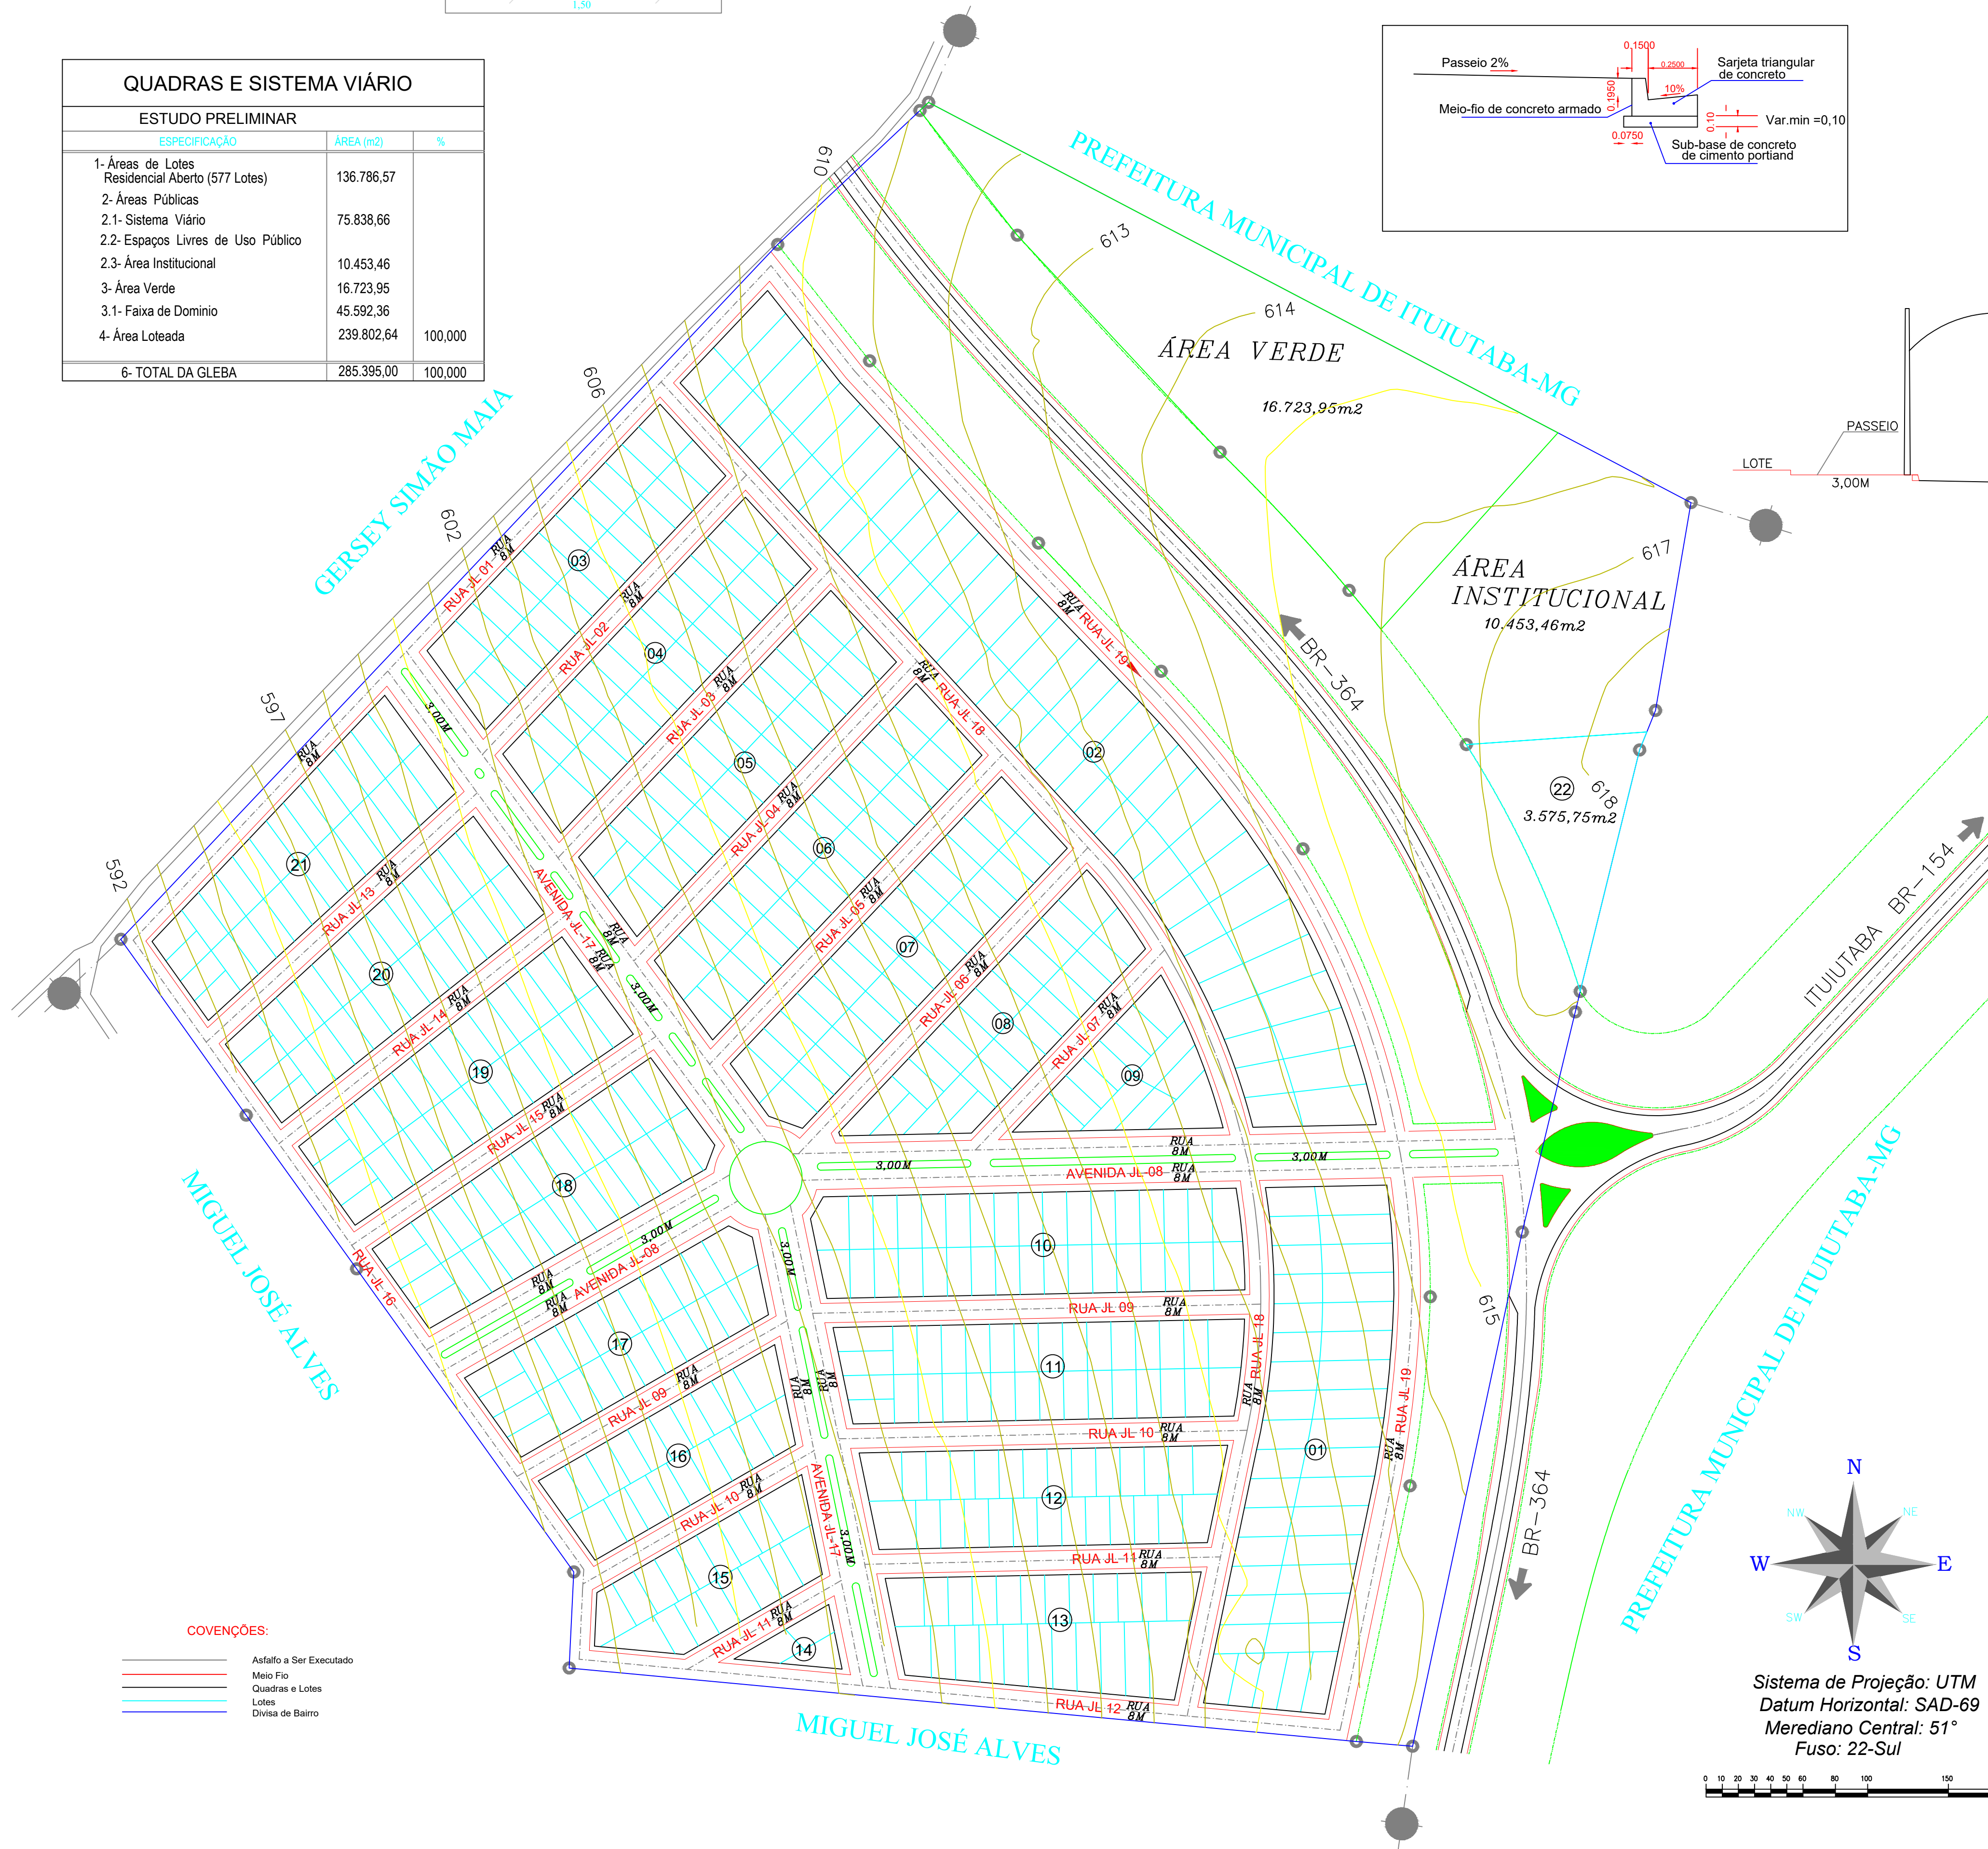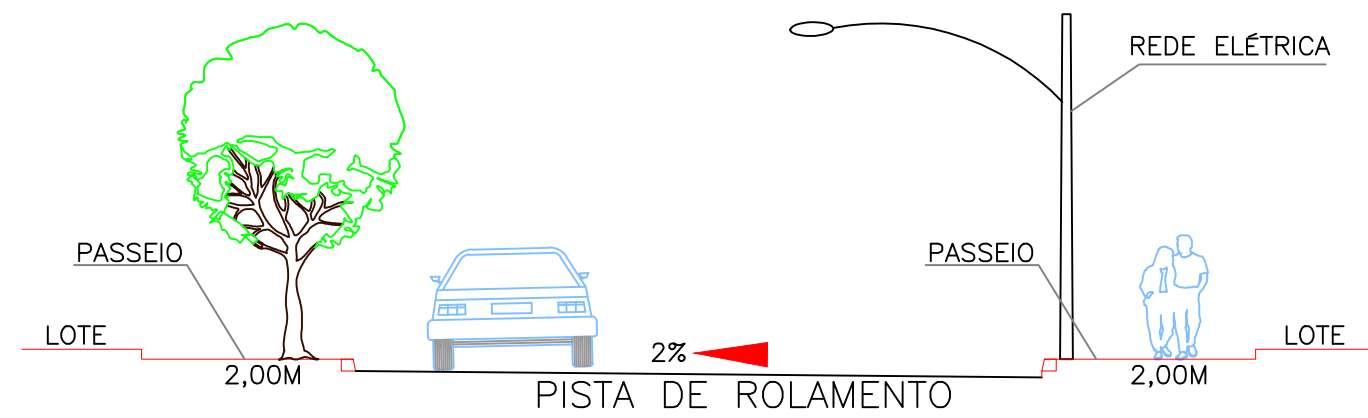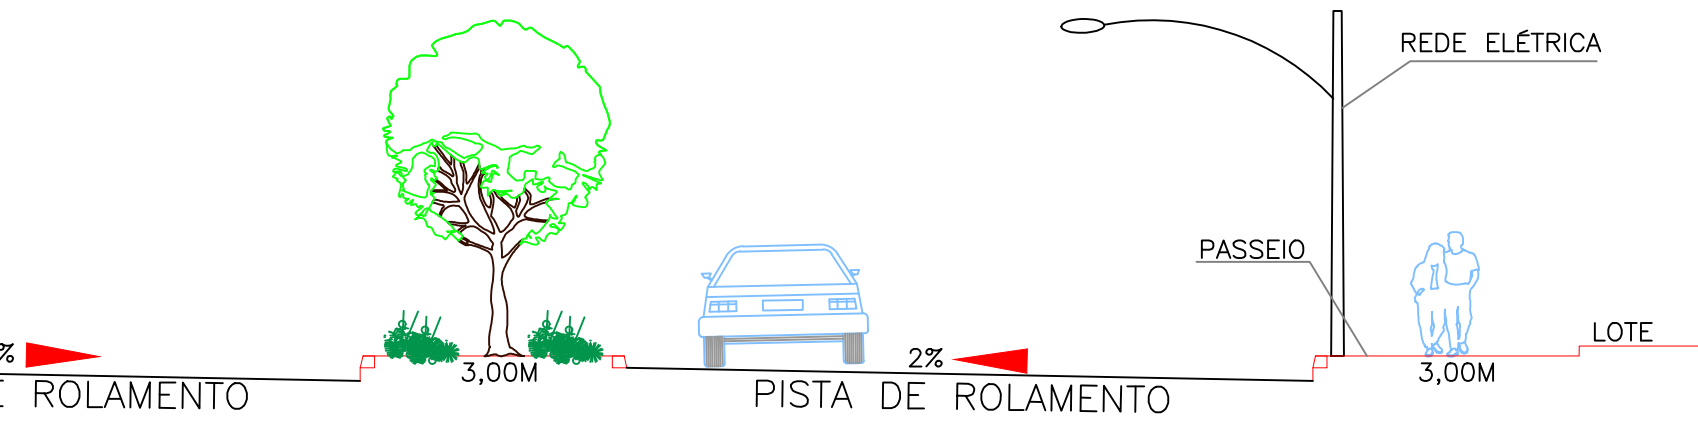

R&S ENGENHARIA LTDA
Rua Eurípedes da Silva Sales 339
São Francisco, Catalão - GO
CEP: 75707-260
(34) 99176-6327

Projeto de Pavimentação

Identificação	Conteúdo Projeto da Malha de Pavimentação
	Local: Residencial Joaquim Leme Obs: Proximo ao Aeroporto Tito Teixeira
	Cidade: Ituiutaba - MG
	Bairro: Residencial Joaquim Leme
Desenho: Hagamenon	Proprietário: C&A Construtora
	Escalas: Indicadas
	Conteúdo: Projeto de Pavimentação e Detalhes
	Aprovação:
Data: Julho/2016	Assinaturas:
	Proprietário: C&A Construtora
	Resp. Técnico: Engº Civil: Clovis Moreira de Barros CREA - MG 75954/D Telef. : (64) 8112-9136 Email : contato@rsengenharia.net