
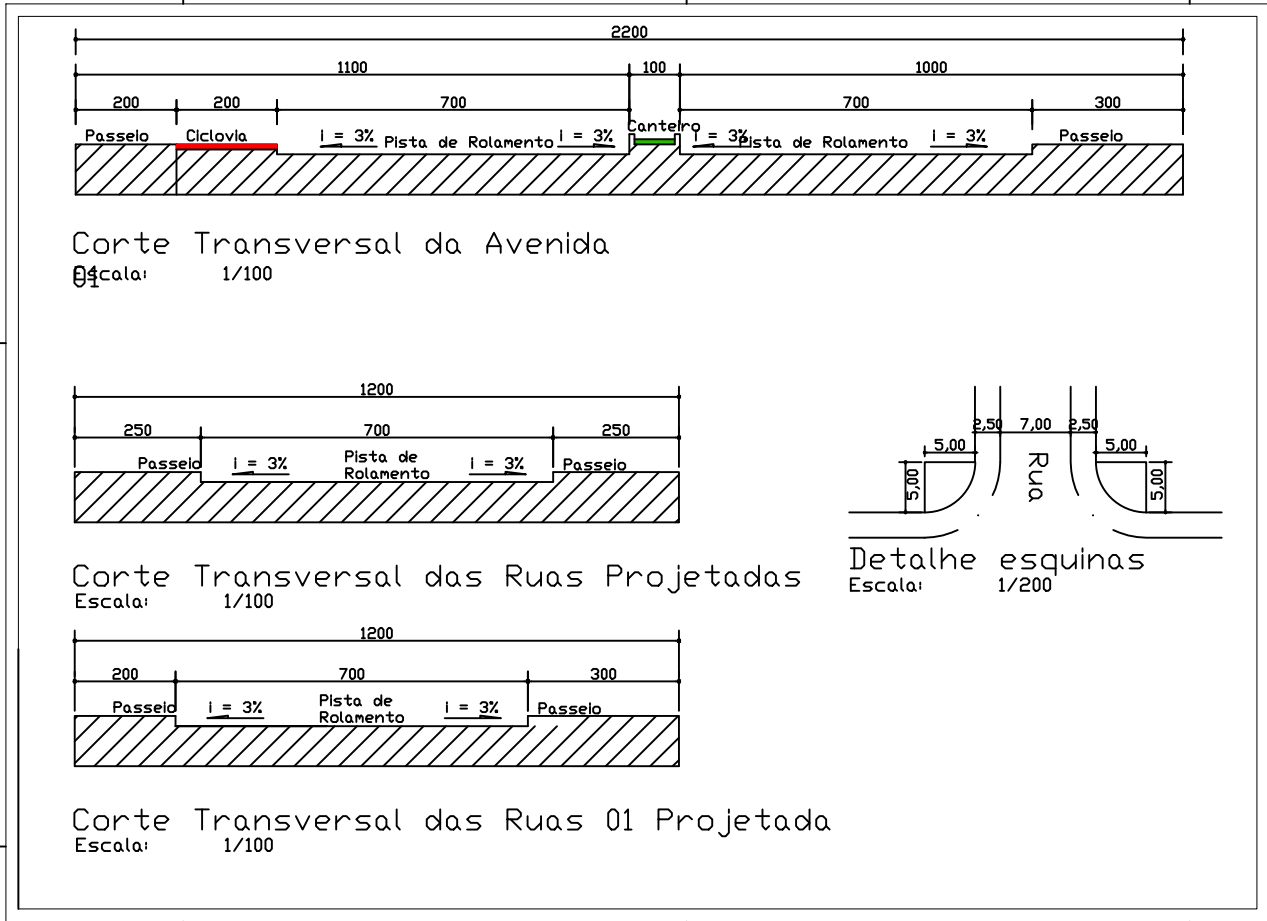


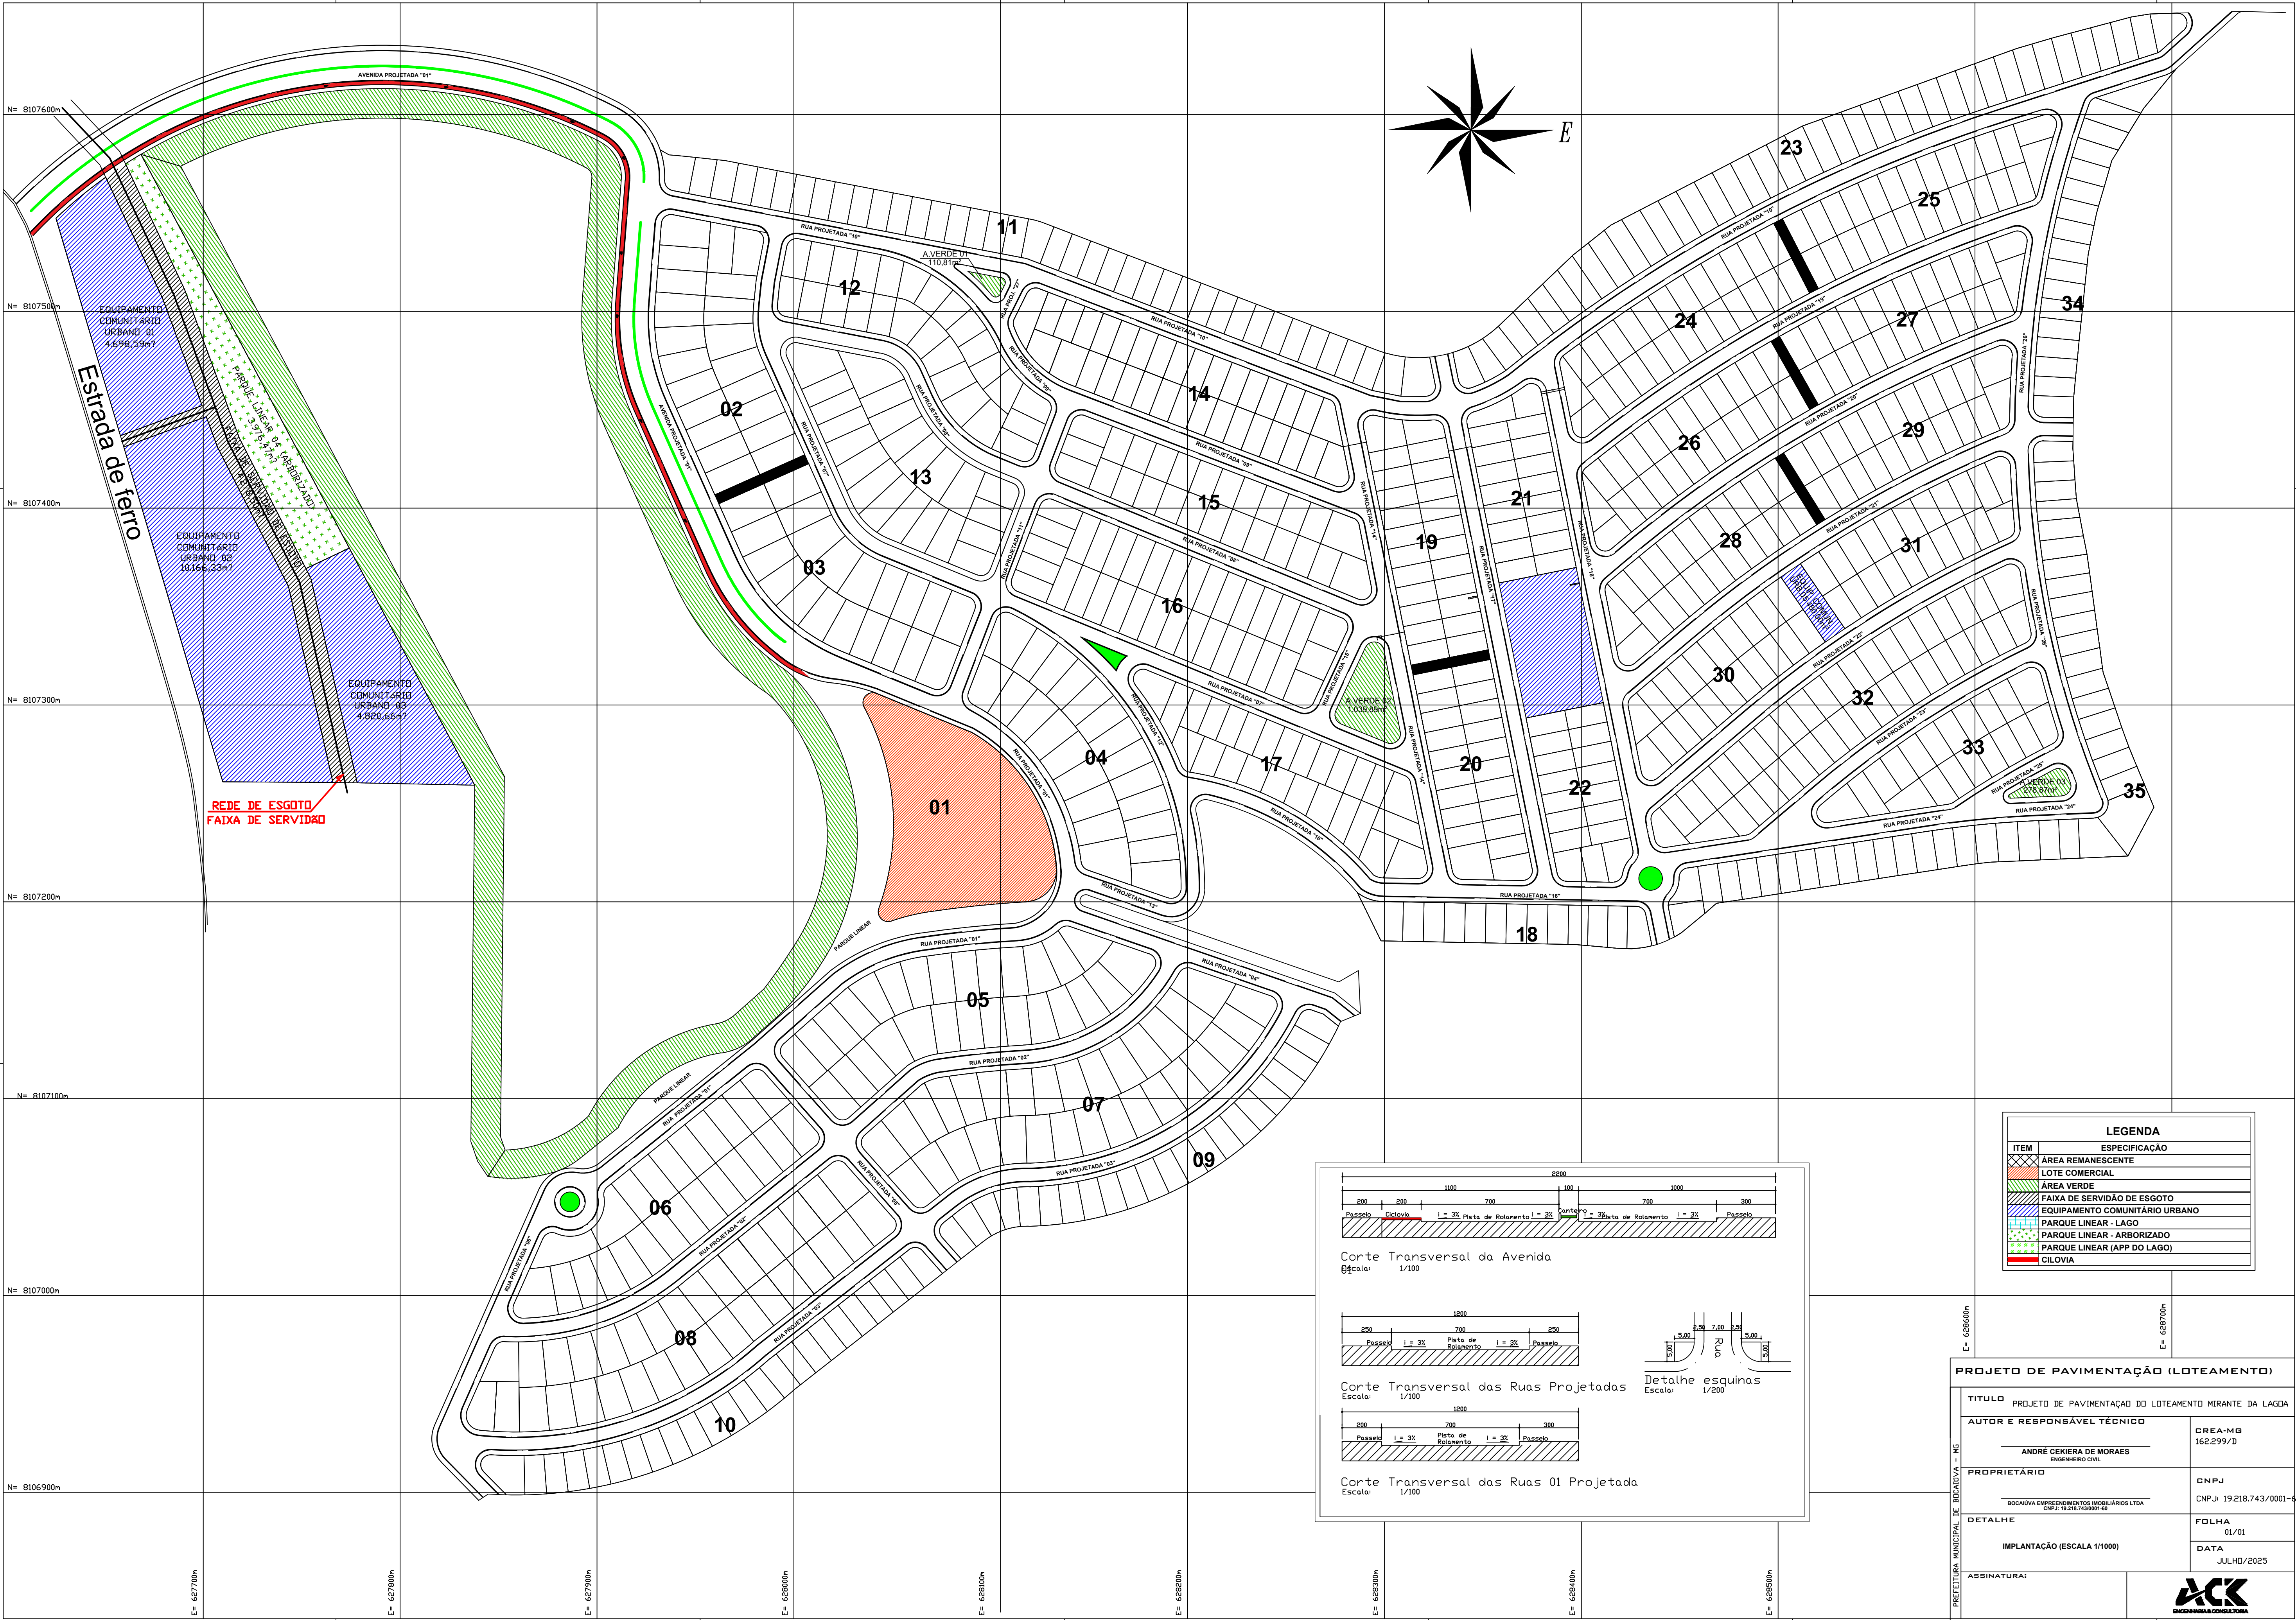

LEGENDA	
ITEM	ESPECIFICAÇÃO
[Symbol]	ÁREA REMANESCENTE
[Symbol]	LOTE COMERCIAL
[Symbol]	ÁREA VERDE
[Symbol]	FAIXA DE SERVIDÃO DE ESGOTO
[Symbol]	EQUIPAMENTO COMUNITÁRIO URBANO
[Symbol]	PARQUE LINEAR - LAGO
[Symbol]	PARQUE LINEAR - ARBORIZADO
[Symbol]	PARQUE LINEAR (APP DO LAGO)
[Symbol]	CILOVIA

PROJETO DE PAVIMENTAÇÃO (LOTEAMENTO)			
TÍTULO		PROJETO DE PAVIMENTAÇÃO DO LOTEAMENTO MIRANTE DA LAGOA	
AUTOR E RESPONSÁVEL TÉCNICO		CREA-MG 162.299/D	
PROPRIETÁRIO		CNPJ 19.218.743/0001-60	
DETALHE		FOLHA 01/01	
IMPLANTAÇÃO (ESCALA 1/1000)		DATA JULHO/2025	
ASSINATURA:		ACK	