


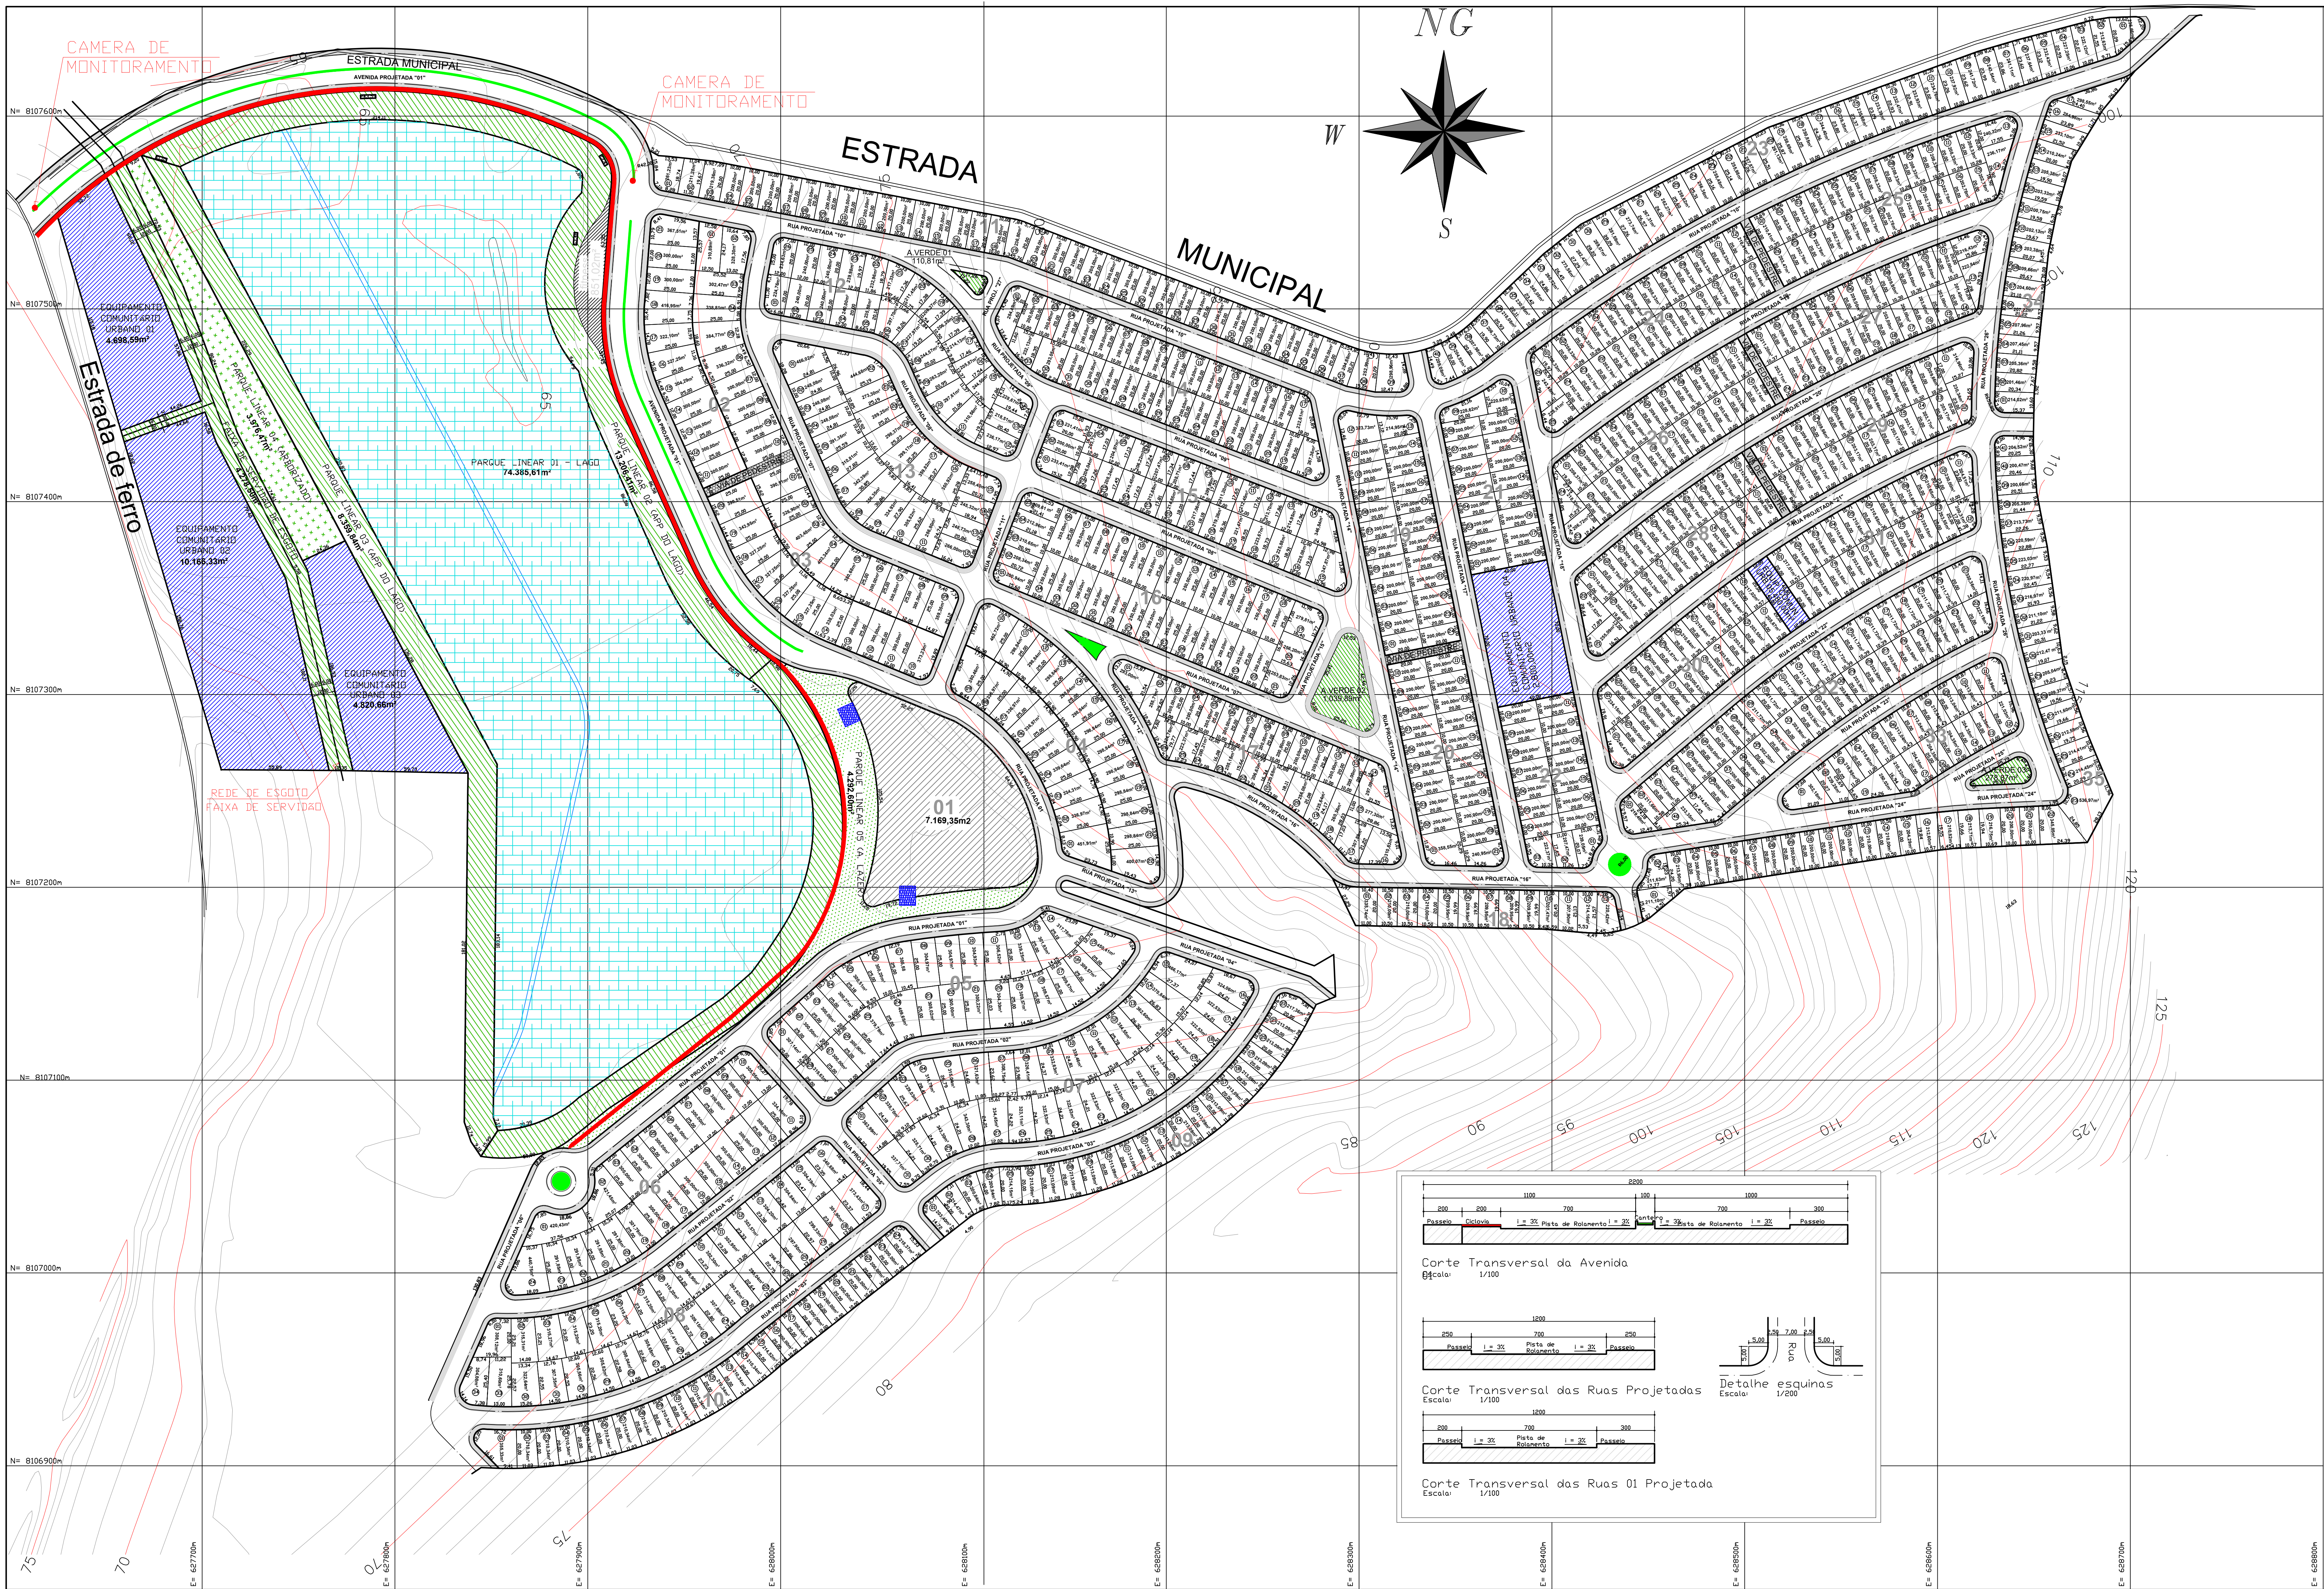

ÁREAS DAS QUADRAS					
DESCRIÇÃO	DE	ATÉ	TOTAL	ÁREAS (m²)	
QUADRA "01"	01	01	01	7.169,38	
QUADRA "02"	01	21	21	6.739,66	
QUADRA "03"	01	20	42	6.818,98	
QUADRA "04"	01	22	64	7.341,20	
QUADRA "05"	01	28	92	8.904,25	
QUADRA "06"	01	24	116	7.591,03	
QUADRA "07"	01	31	147	10.432,80	
QUADRA "08"	01	34	181	10.539,41	
QUADRA "09"	01	22	203	4.660,50	
QUADRA "10"	01	24	227	5.122,64	
QUADRA "11"	01	39	266	8.048,70	
QUADRA "12"	01	26	292	6.199,07	
QUADRA "13"	01	22	314	6.862,67	
QUADRA "14"	01	33	347	6.909,64	
QUADRA "15"	01	26	373	5.840,54	
QUADRA "16"	01	34	407	8.332,34	
QUADRA "17"	01	26	433	5.963,69	
QUADRA "18"	01	13	446	2.859,44	
QUADRA "19"	01	24	470	4.938,68	
QUADRA "20"	01	21	491	4.399,50	
QUADRA "21"	01	18	509	3.649,25	
QUADRA "22"	01	17	526	3.468,89	
QUADRA "23"	01	40	566	9.753,96	
QUADRA "24"	01	26	592	5.408,31	
QUADRA "25"	01	26	618	5.412,58	
QUADRA "26"	01	24	642	4.959,39	
QUADRA "27"	01	24	666	4.965,61	
QUADRA "28"	01	22	688	4.655,88	
QUADRA "29"	01	22	710	4.677,00	
QUADRA "30"	01	21	731	4.356,53	
QUADRA "31"	01	21	752	4.371,09	
QUADRA "32"	01	40	792	8.527,73	
QUADRA "33"	01	19	811	4.256,65	
QUADRA "34"	01	17	828	3.699,57	
QUADRA "35"	01	41	869	8.998,27	
TOTAL			869	216.834,83	

ITEM	ESPECIFICAÇÃO
[Pattern]	ÁREA REMANESCENTE
[Pattern]	LOTE COMERCIAL
[Pattern]	ÁREA VERDE
[Pattern]	FAIXA DE SERVIÇÃO DE ESGOTO
[Pattern]	EQUIPAMENTO COMUNITÁRIO URBANO
[Pattern]	PARQUE LINEAR - LAGO
[Pattern]	PARQUE LINEAR - ARBORIZADO
[Pattern]	PARQUE LINEAR (APP DO LAGO)
[Pattern]	PARQUE LINEAR (LAZER)
[Pattern]	CILOVIA
[Pattern]	ÁREA DE POÇOS

PROJETO URBANÍSTICO (LOTEAMENTO)

ÁREA TOTAL DO LOTEAMENTO : 45.3329 ha (453.329,59 m²)

ITEM	ESPECIFICAÇÃO	ÁREA (m²)	%
1	ÁREA DOS LOTES (869 LOTES)	216.834,83	47,83
2	ÁREAS PÚBLICAS	236.494,76	52,17
2.1	SISTEMA VIÁRIO TOTAL	106.857,66	23,57
2.1.1	SISTEMA VIÁRIO	102.579,16	-
2.1.2	FAIXA DE SERVIÇÃO DE ESGOTO	4.278,50	-
2.2	ÁREAS DE EQUIPAMENTOS COMUNITÁRIOS	22.965,58	5,07
2.2.1	ÁREA DE EQUIPAMENTO COMUNITÁRIO URBANO 01	4.698,59	-
2.2.2	ÁREA DE EQUIPAMENTO COMUNITÁRIO URBANO 02	10.166,23	-
2.2.3	ÁREA DE EQUIPAMENTO COMUNITÁRIO URBANO 03	4.820,66	-
2.2.4	ÁREA DE EQUIPAMENTO COMUNITÁRIO URBANO 04	2.800,00	-
2.2.5	ÁREA DE EQUIPAMENTO COMUNITÁRIO URBANO 05	480,00	-
2.3	ÁREA DE POÇOS - DOAÇÃO SAAE	170,00	-
2.3.1	ÁREA DE POÇO	85,00	-
2.3.2	ÁREA DE POÇO	85,00	-
2.4	ÁREAS VERDES	1.429,57	0,32
2.5	(PARQUE LINEAR)	104.220,93	22,99
2.5.1	(PARQUE LINEAR 01 - LAGO)	74.385,61	-
2.5.2	(PARQUE LINEAR 02 E 03 - APP DO LAGO)	21.566,25	-
2.5.3	(PARQUE LINEAR 04 - ARBORIZADO)	3.976,47	-
2.5.4	(PARQUE LINEAR 05 - ÁREA DE LAZER)	4.292,60	-
2.6	ESPAÇO FITNESS	851,02	0,19
4	ÁREA LOTEADA	453.329,59	100,00

TÍTULO	PROJETO URBANÍSTICO DO LOTEAMENTO MIRANTE DA LAGOA
AUTORA E RESPONSÁVEL TÉCNICO	CAU A-154467-5
PROPRIETÁRIO	Laura M. M. V. Gomes
DETALHE	IMPLANTAÇÃO (ESCALA 1/1000)
LEGENDA:	REVISÃO: 01/01