


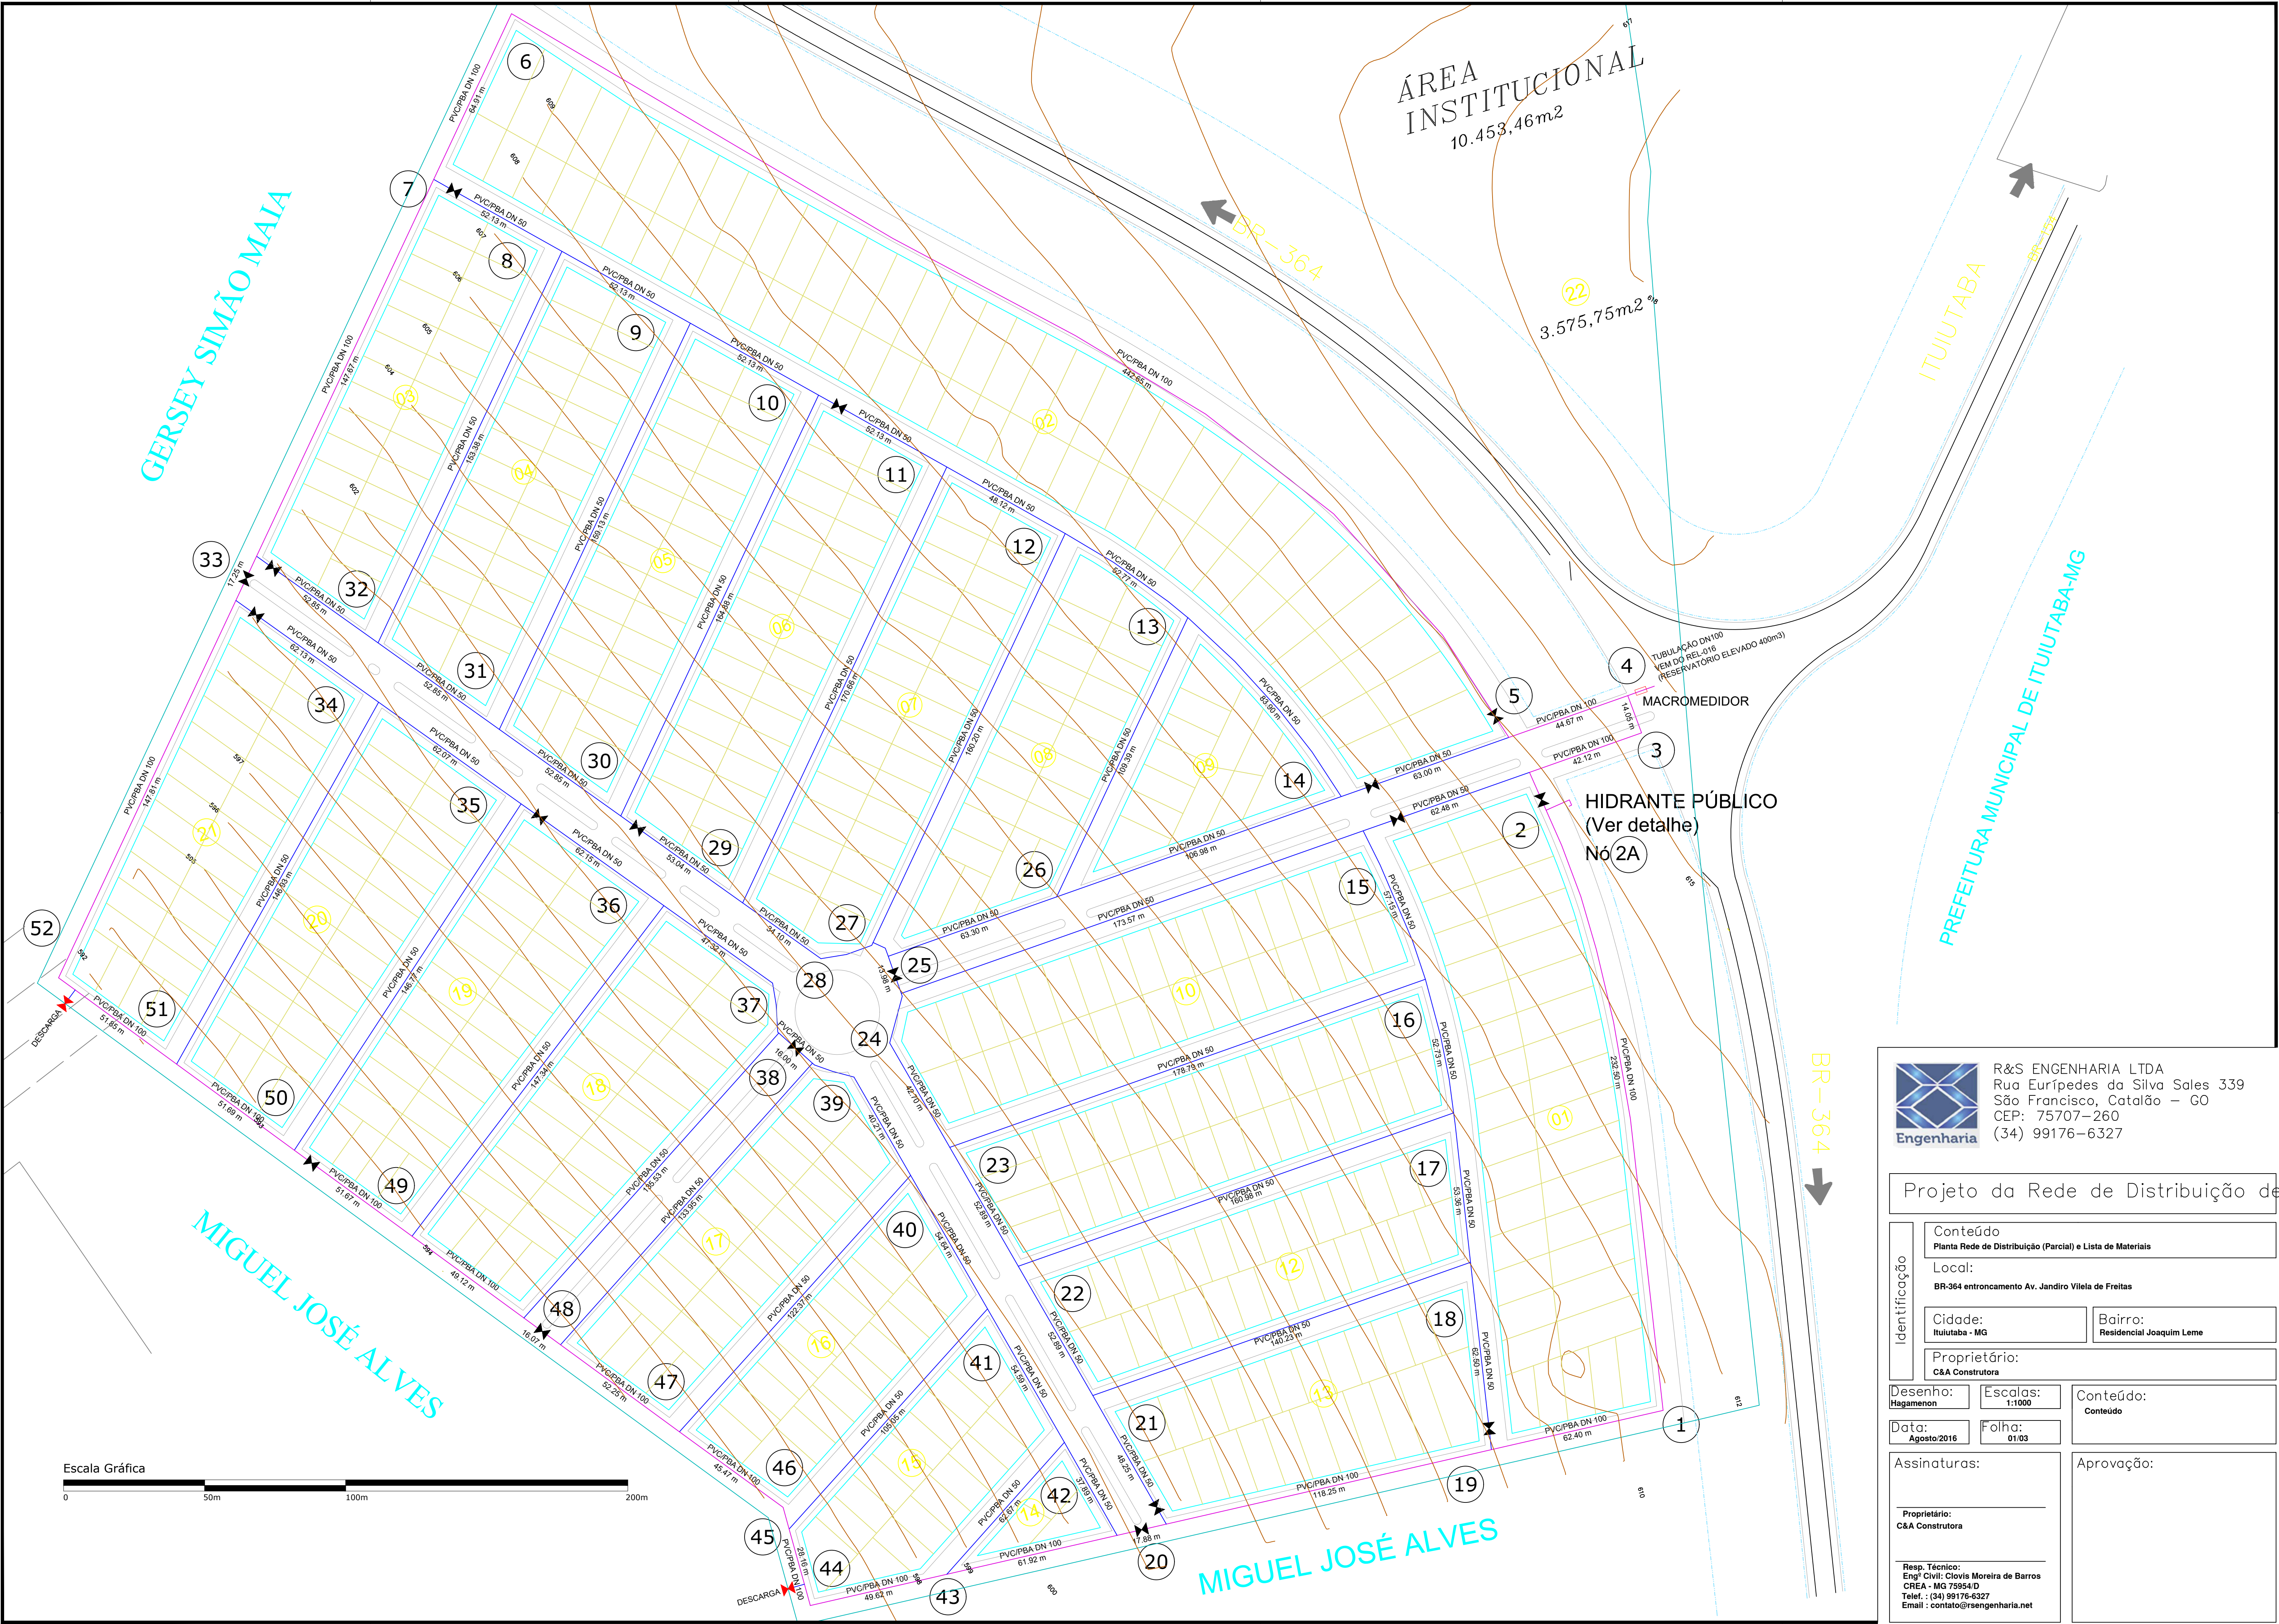

R&S ENGENHARIA LTDA  
Rua Eurípides da Silva Sales 339  
São Francisco, Catalão - GO  
CEP: 75707-260  
(34) 99176-6327

Projeto da Rede de Distribuição de Água

|                 |                                                            |
|-----------------|------------------------------------------------------------|
| Identificação   | Conteúdo                                                   |
|                 | Planta Rede de Distribuição (Parcial) e Lista de Materiais |
|                 | Local:                                                     |
|                 | BR-364 entroncamento Av. Jandiro Vilela de Freitas         |
| Cidade:         | Bairro:                                                    |
|                 | Residencial Joaquim Leme                                   |
| Proprietário:   |                                                            |
| C&A Construtora |                                                            |

|             |          |           |
|-------------|----------|-----------|
| Desenho:    | Escalas: | Conteúdo: |
| Hagamenon   | 1:1000   |           |
| Data:       | Folha:   | Conteúdo  |
| Agosto/2016 | 01/03    |           |

|   |            |
|---|------------|
| Assinaturas:   | Aprovação: |
| <div>Proprietário:<br/>C&amp;A Construtora</div> <div>Resp. Técnico:<br/>Engº Civil: Clóvis Moreira de Barros<br/>CREA - MG 75954/D<br/>Telef. : (34) 99176-6327<br/>Email : contato@rsengenharia.net</div> |            |