


MAPA DE INFLUÊNCIA
Sem escala

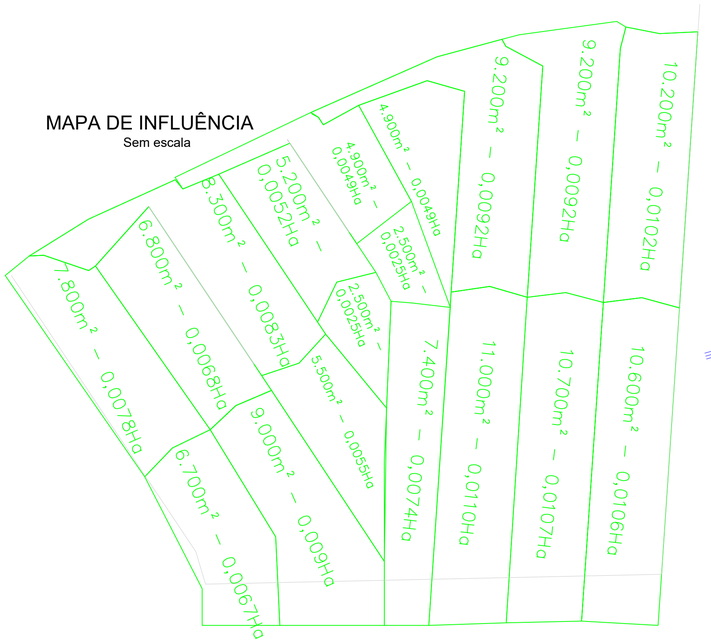


DETALHE BOCA-DE-LOBO SIMPLES

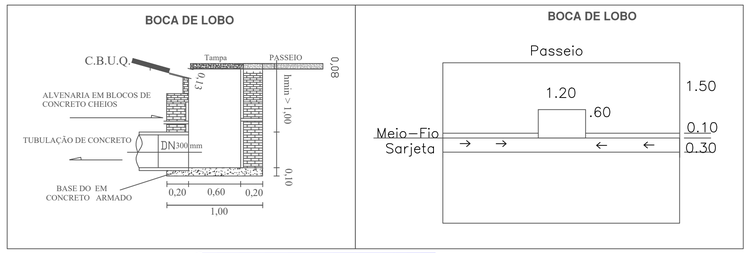


POÇO-DE-VISITA

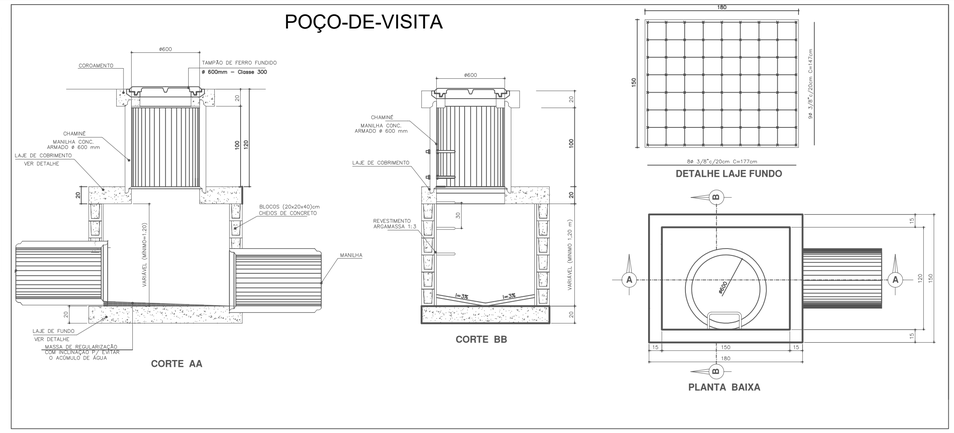


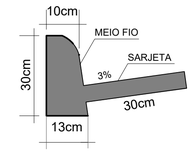

Detalhe - Sarjeta
Sem escala

BL`S BOCA DE LOBO

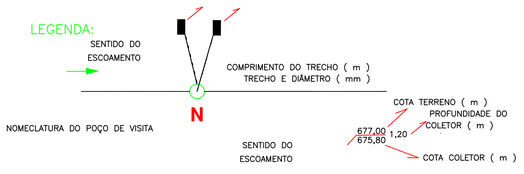

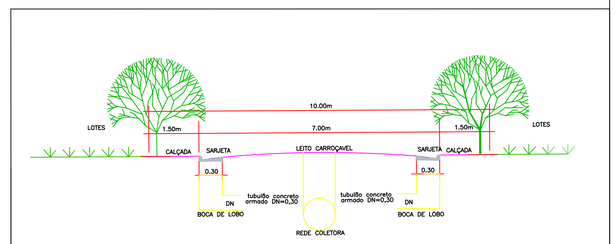

A PERFIL "A" - PADRÃO VIAS LOCAIS

MAPA DA REDE
escala 1:1000

PAULO CESAR VALIM CESARINO
MAT. 8576

JOSÉ ITAMAR FERREIRA
MAT. 12.084

JOSÉ ITAMAR FERREIRA
MAT. 12.084

Tubulação Concreto

tubo 300mm	sem armação	350,00m-ramal
tubo 400mm	sem armação	1180,00 m
tubo 600mm	sem armação	252,00 m
tubo 800mm	com armação	393,00 m

QUADRO DE LOTES

LOTES	364	

Gleba(escriturada) (Matrícula 13.748)	12 ha	
Área dos Lotes	74.913,05m²	62,43 %
Rua - Pavimentação	22.609,26m²	18,84 %
Calçadas e Sarjetas	10.129,76m²	8,44 %
Áreas Institucionais	8.743,13 m²	7,29%
Praças -	3.604,80 m²	3,00%
		10,29%
Gleba -	120.000,00 m²	100,00 %
Acesso rodovia e estrada	2865,10 m²	extra

"PARQUE DAS NAÇÕES "
LOTEAMENTO

FOLHA: 01/01

DETALHE: Projeto Drenagem

PROPRIETÁRIO: JOSÉ ITAMAR FERREIRA — CPF: 096.878.746-00

revisão 3 - 15 de abril de 2019

ENDEREÇO: Sitio Bairro Alto - CAMPANHA/ MG

NÚMERO DA ART:

PROPRIETARIO :

JOSÉ ITAMAR FERREIRA - PP: GUILHERME ROMERO
CPF:096.878.746-00

Autor do Projeto :

Rafael Amaral Barbosa
Engenheiro Civil
Crea: 196.069/D

PREFEITURA :