



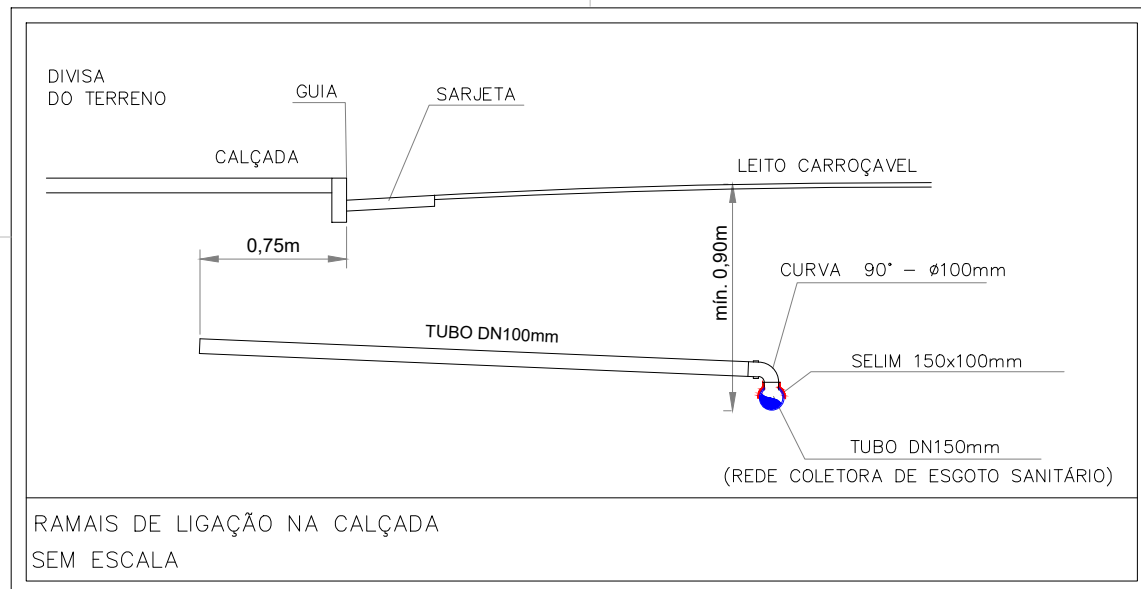

RELAÇÃO DE MATERIAL			
ITEM	DESCRIÇÃO	UNID.	QUANT.
01	TUBO DN 150mm PVC CLASSE 15 (REDE COLETORA)	m	3.155,55
03	TUBO DN 100mm PVC CLASSE 15 (RAMAL DE LIGAÇÃO)	m	1.470,00
04	CURVA 90° - Ø100mm CLASSE 15	peça	361,00
05	SELIM 150mm x 100 mm	peça	361,00
06	PV - POÇO DE VISITA	UNID.	50,00
07	CAP PVC 100 mm	peça	361,00
08	Tampão Ferro F*F* T-109	peça	50,00


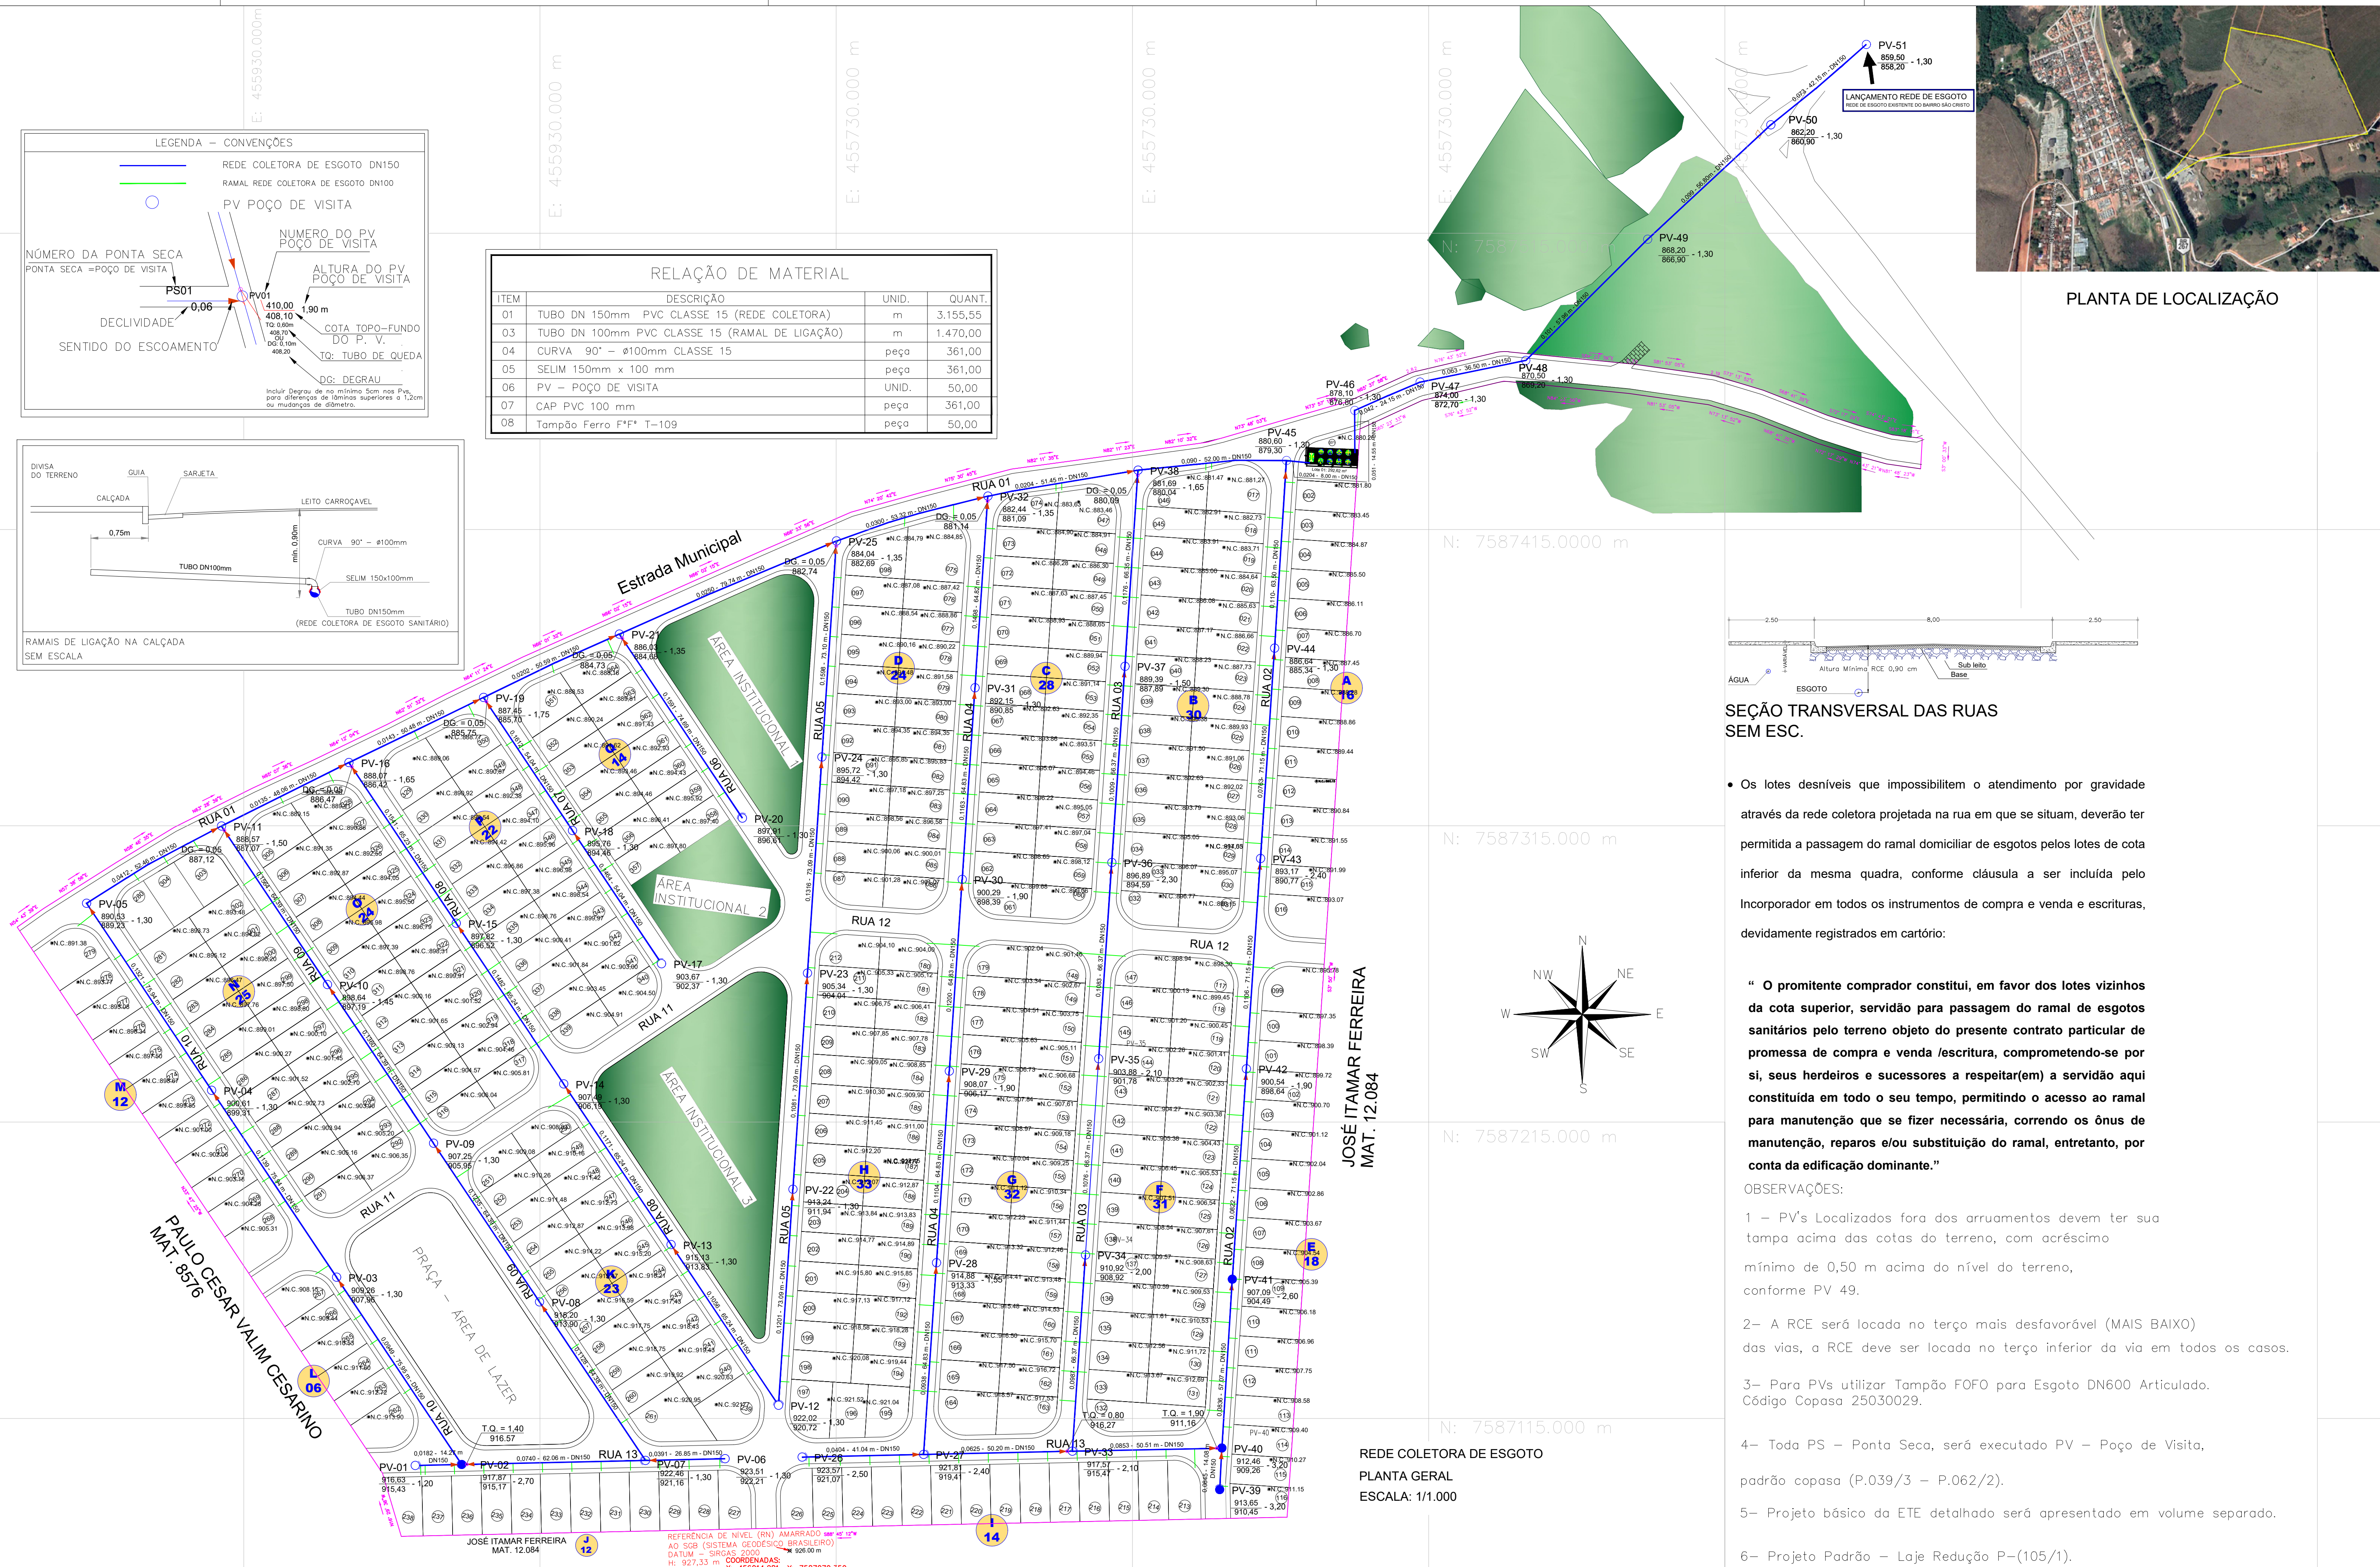


APLICAÇÃO	ASSUNTO
-----------	---------

CLASSIFICAÇÃO	a				
	b				
	c				
		DATA	EXECUT.	VISTO	APROV.
	ALTERAÇÕES				

NOTAS:

- 1- O MATERIAL DOS TRECHOS SERÃO EM TUBO PVC, CONFORME NBR 7362 DA ABNT.
- 2- TODAS AS CONEXÕES DE PVC OU FFP (TÊS E CURVAS) DEVERÃO SER ANCORADOS COM BLOCOS DE ANCORAGEM;
- 3- O DIMENSIONAMENTO DAS REDES COLETORAS DE ESGOTOS FORAM CALCULADAS EM RELAÇÃO A COTA ALTIMÉTRICA DO TERRENO, CASO VENHA ALTERAR OS GREIDES DOS ARRUMAMENTOS DO LOTEAMENTO EM QUESTÃO, DEVERÁ SER REALIZADA ANTES DA EXECUÇÃO DAS REDES, A ELABORAÇÃO DA NOTA DE SERVIÇO E LEVANTAMENTO DE NORMAIS.
- 4- LOCAR OS RAMAIS DA REDE DE ESGOTO DE 100mm PUXANDO 1 METRO DA DIVISA DO LOTE NO PONTO MAIS BAIXO.
- 5- O EMPREENDIMENTO CONSTITUI-SE DE UMA ÚNICA SUB-BACIA.

 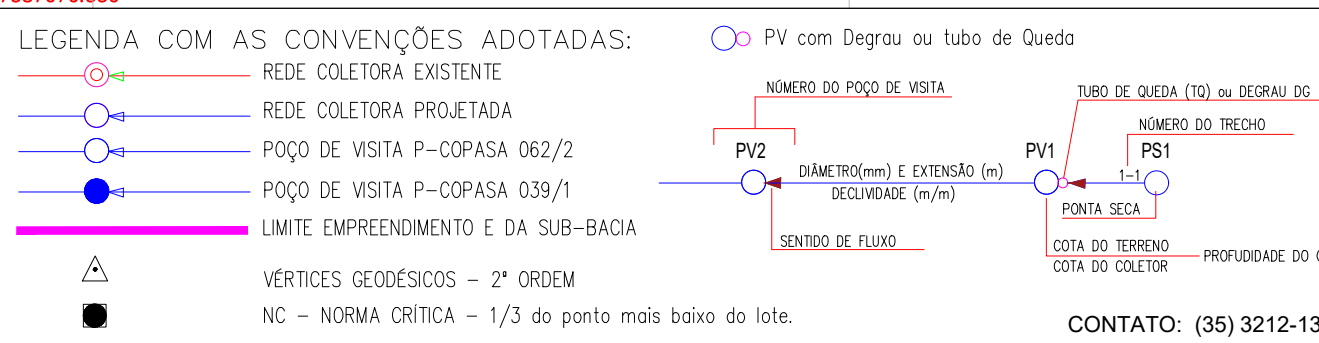

PARCEL
ENGENHARIA

(35) 99713-0102 EMAIL: Parcel.engenharia@gmail.com

LOTEAMENTO PARQUE DAS NAÇÕES				COMPANHIA DE SANEAMENTO DE MINAS GERAIS CAMPANHA - MG		ESCALA 1/1000	
RT	ASSINATURA Engenheiro Civil: Samuel Silva Moraes	CREA 226056/D		VISTO	SISTEMA DE ESGOTOS SANITÁRIOS RESIDENCIAL PARQUE DAS NAÇÕES REDE COLETORA DE ESGOTO SANITÁRIO PLANTA CONSTRUTIVA	Nº 03	P.E.
PROJ.		VISTO:		APROV.:			
DES.		VISTO:		DATA: JANEIRO / 2020			
						FOLHA 03 DE 03	