

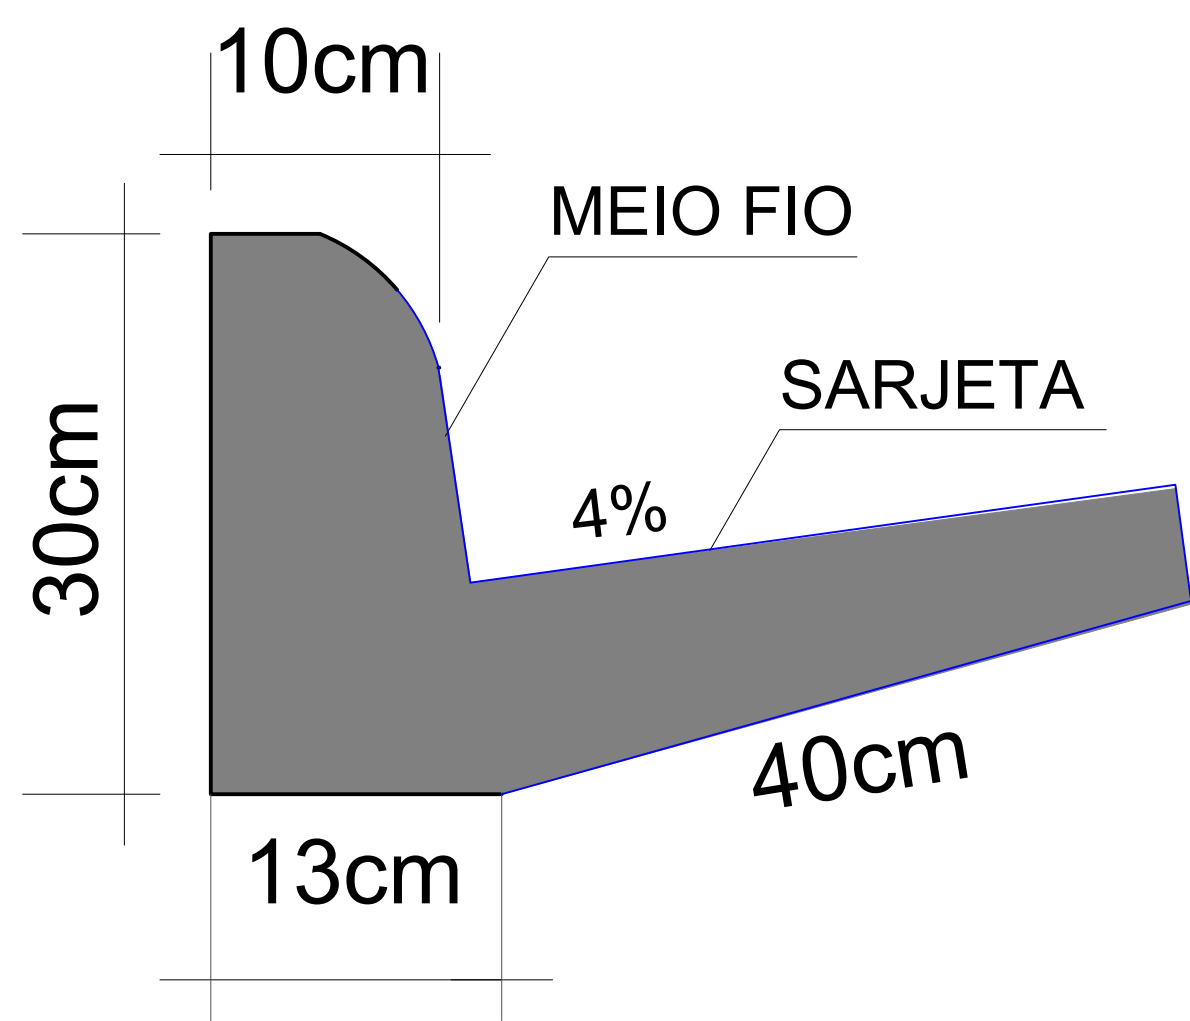


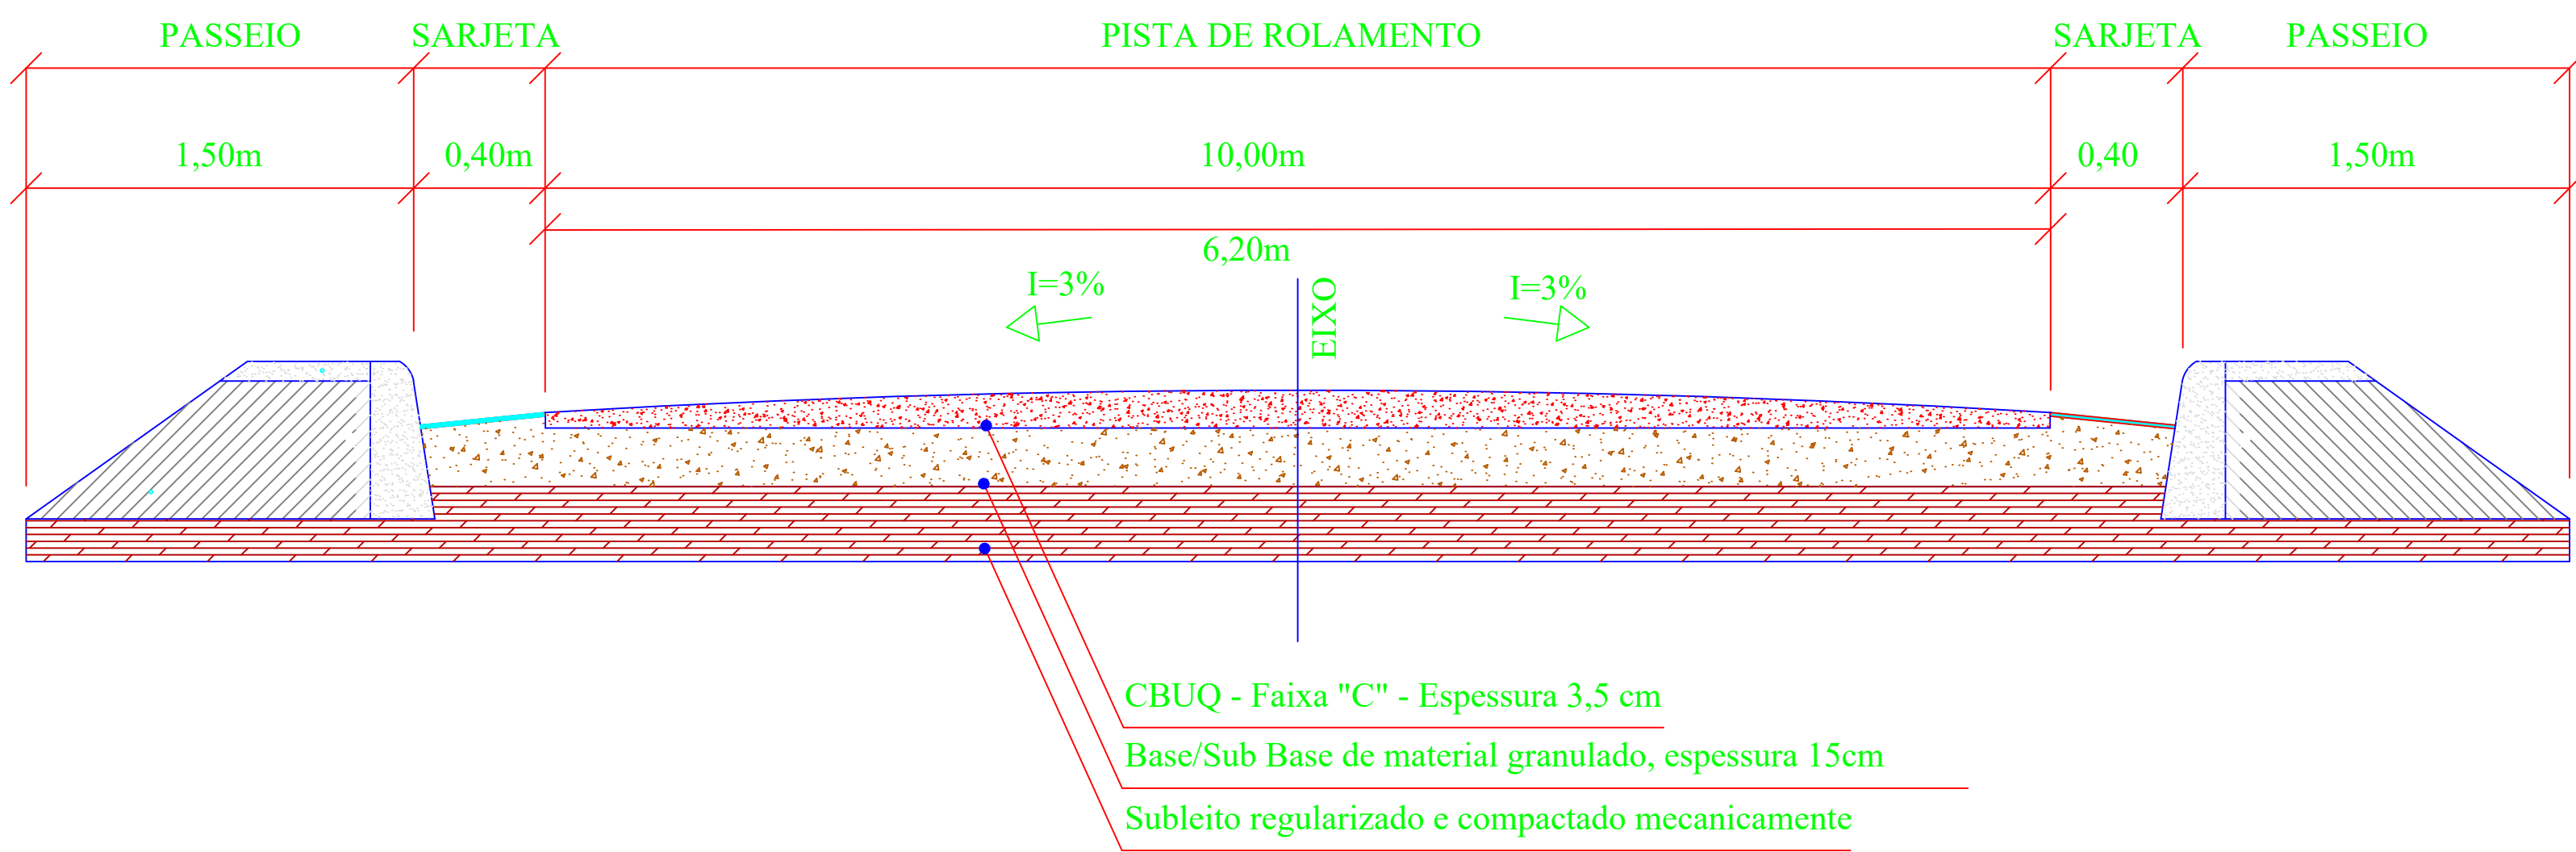

Detalhe - Sarjeta
Sem escala

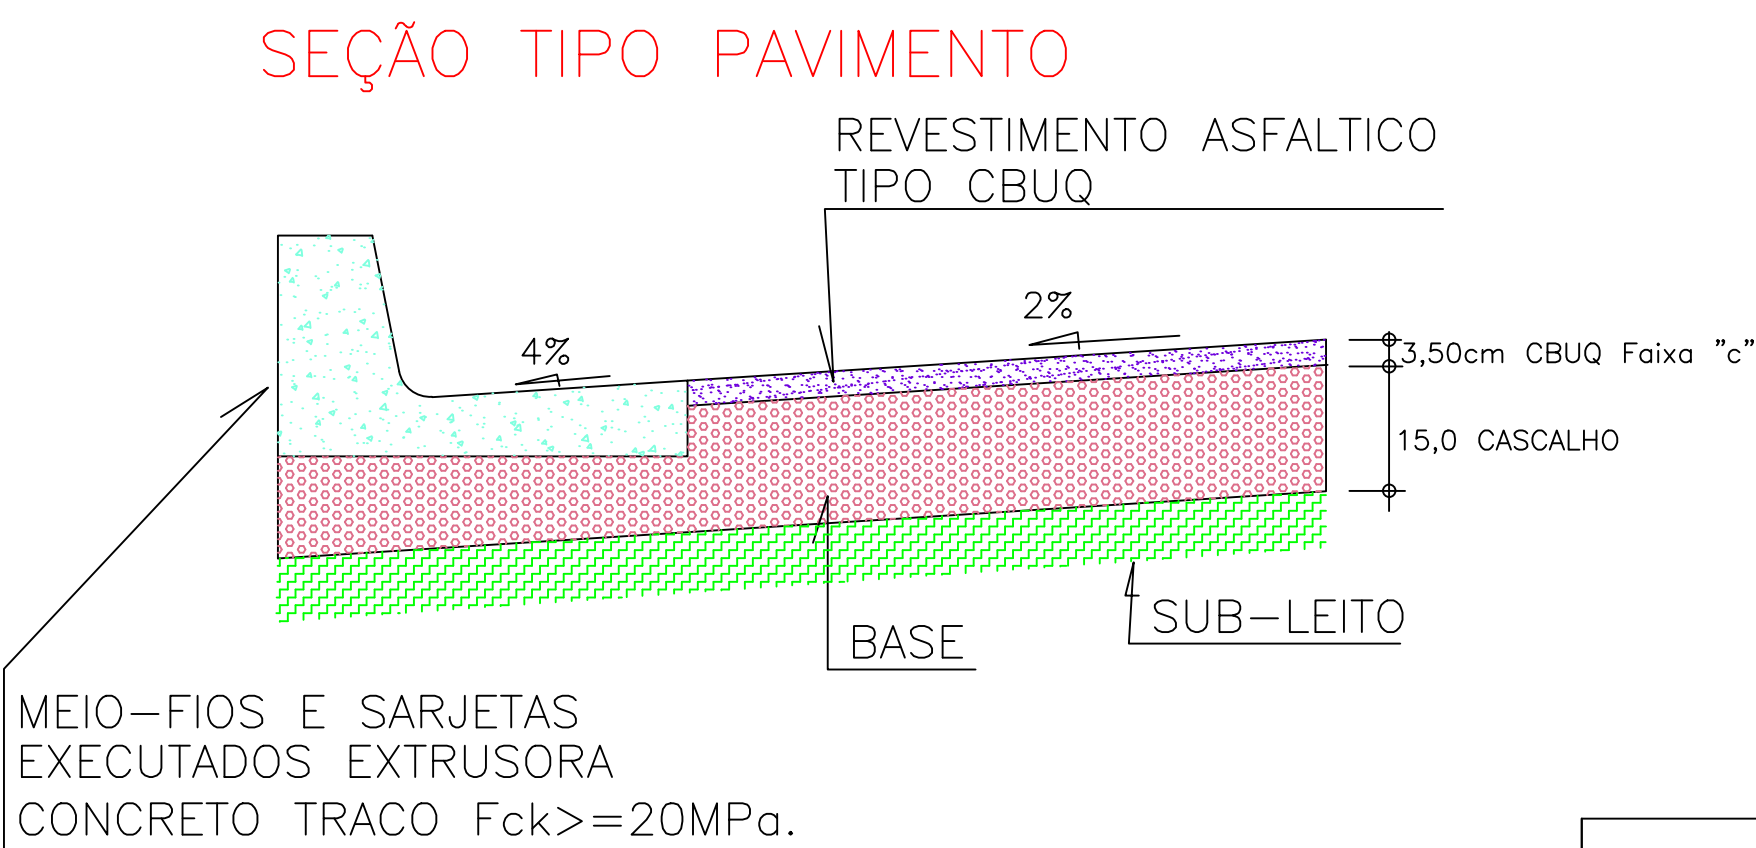

TÍTULO: "PARQUE DAS NAÇÕES " LOTEAMENTO		FOLHA: 01/01
DETALHE: Projeto Sinalização Viária		
PROPRIETÁRIO:	MIFE NEGOCIOS IMOBILIARIOS LTDA	CNPJ: 37.014.492/0001-84
ENDEREÇO: Sítio Bairro Alto - CAMPANHA/ MG		
		C:\Users\Bafun\Desktop\city - empreendimentos\logomarca - sky.jpg
NÚMERO DA ART:		
PROPRITARIO : MIFE NEGOCIOS IMOBILIARIOS LTDA CNPJ: 37.014.492/0001-82		
Autor do Projeto : ----- Rafael Amaral Barbosa Engenheiro Civil Crea: 196.069/D		
PREFEITURA :		