


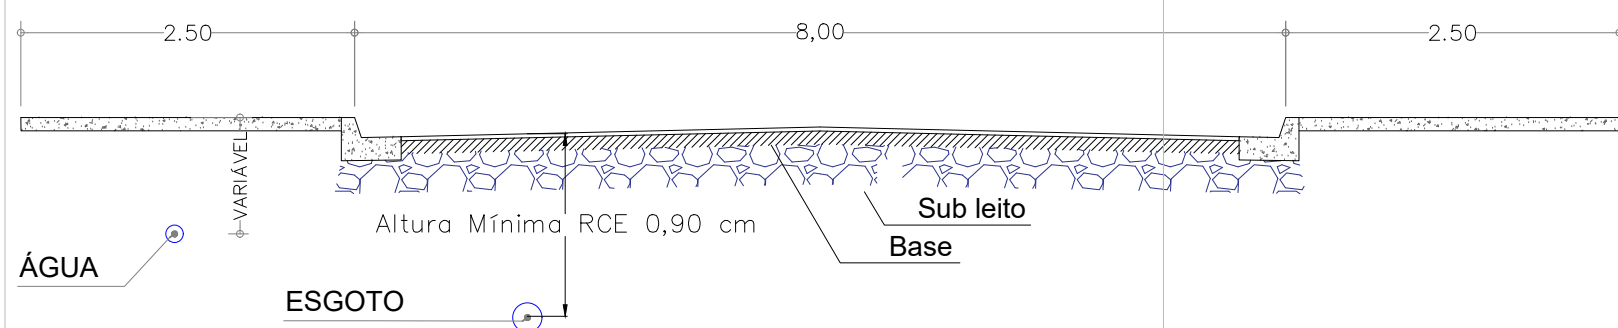

SEÇÃO TRANSVERSAL DAS RUAS SEM ESC.

CURVAS DE NÍVEL

- Curva de nível mestra
- Curva de nível secundária

REDE ABASTECIMENTO DE ÁGUA
PLANTA GERAL
ESCALA: 1/1.000

CLASSIFICAÇÃO	ASSUNTO			
	APLICAÇÃO			
	ALTERAÇÕES			
a				
b				
c				
	DATA	EXECUT.	VISTO	APROV.

Notas:1 -Tubulação da Rede de distribuição será da Classe (≥20) conforme item 5.1 alínea p da norma técnica COPASA T.104/2;
2 - Prever Poço seco nas descargas;
3 - Ficar atento na instação do TÊ PVC e JE BBB REDUÇÃO;
4 - Todas as conexões de PVC ou FFP (TÊS, CURVAS,...) deverão ser ancorados com bloco de ancoragem, no memorial descritivo sobre planilha de cálculo RDA está o dimensionamento das ancoragens nos nº, e anexado projeto detalhado de ancoragem das RDA.

5 - Será executado Poço seco nas descargas, projeto padrão COPASA.
6 - Profundidade mínima rede distribuição no passeio 0,90 m.

Profundidade mínima rede adutora nas ruas 1,30 m.

Convenções:

- REGISTRO DE MANOBRA 50mm PROJETO PADRÃO 05.16.005/0
- REGISTRO DE MANOBRA 75mm PROJETO PADRÃO 05.16.005/0
- REGISTRO DE DESCARGA E POÇO SECO - PROJETO PADRÃO 05.16.005/0 E P - 348/0

SENTIDO DA REDE

HIDRANTE

REDE ABASTECIMENTO DE ÁGUA - PVC DN 50 mm

REDE ABASTECIMENTO DE ÁGUA - PVC DN 75mm

REDE ABASTECIMENTO DE ÁGUA - PVC DN 100 mm

REDE ADUTORA PVC-O DE ÁGUA DN 150 mm

Válvula Redutora de Pressão
VRP 1: 12 m.c.a
PS - POÇO SECO

LOTEAMENTO PARQUE DAS NAÇÕES

ASSINATURA
PROJ. Engenheiro Civil: Marcel Gustavo Vitor

CREA
215510/0

VISTO:

APROV.:

DATA:
FEVEREIRO / 2020

COMPANHIA DE SANEAMENTO DE MINAS GERAIS
CAMPANHA - MG

SISTEMA DE ABASTECIMENTO DE ÁGUA
RESIDENCIAL PARQUE DAS NAÇÕES
PLANTA GERAL

ESCALA
1/1000

Nº
01

FOLHA
01 DE 03

P.E.